PRITPAL
CHANA
ARCHITECTS

-DESIGN DRAWINGS-

01 | Location Plan
00-198 | 1:1250@A3

Scale 1250
0 25 50 75

PRITPAL CHANA ARCHITECTS
E: projects@PCarchitects.co.uk
T: 0121 827 5450
W: PCarchitects.co.uk
ARB: 085131K
RIBA: 20015990

1. ALL DIMENSIONS ARE IN MM UNLESS OTHERWISE STATED.
2. DO NOT SCALE DRAWINGS, FIGURED DIMENSIONS TO BE USED ONLY.
3. ALL DETAILS AND DIMENSIONS ARE TO BE CONFIRMED ON SITE, PRIOR TO WORKS COMMENCING OR ANY ORDERING OF MATERIALS.
4. THE CONTRACTOR MUST INFORM THE ARCHITECT OF ANY DISCREPANCIES FOR CLARIFICATION BEFORE PROCEEDING.
5. THE SOLE PURPOSE OF THE DRAWING IS FOR THE ISSUE STATUS ONLY.

CLIENT
Dr. Sabur Malek

PROJECT
65, Sir Harrys Road, B15 2UX

DRAWING TITLE
Location Plan

ISSUE STATUS
PLANNING PERMISSION

SCALE	DRAWN	CHECKED	DATE
1:1250 @A3	JAA	PC	09.10.25

JOB NO.	DRG. NO.	REVISION
621	621-00-198	-

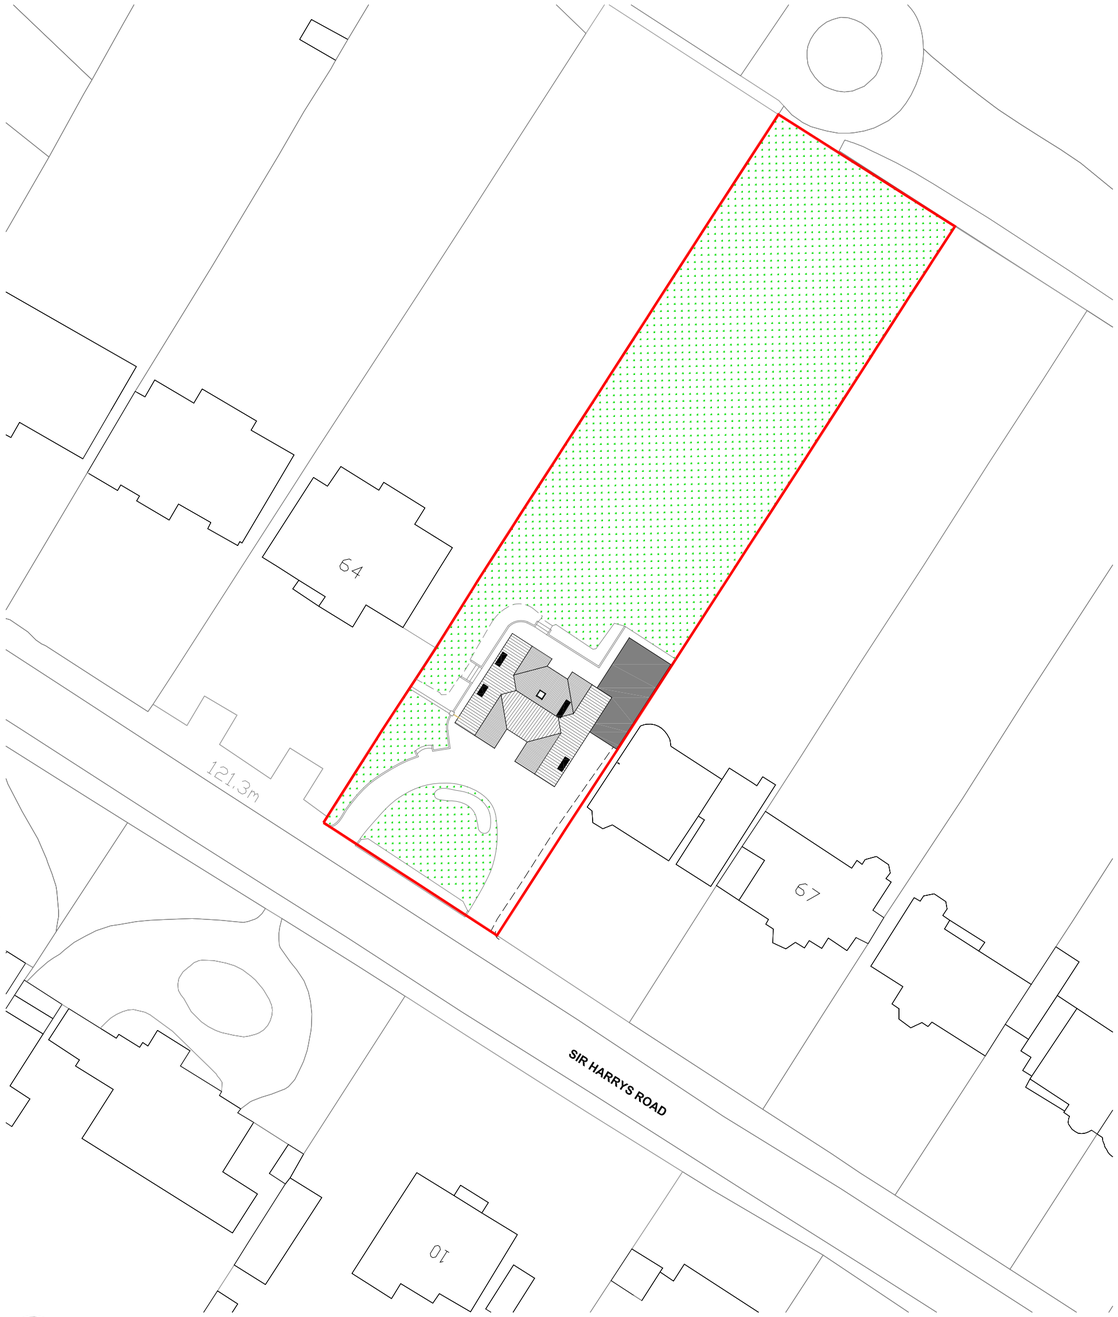

01 Existing Site Plan
00-099 1:500@A2

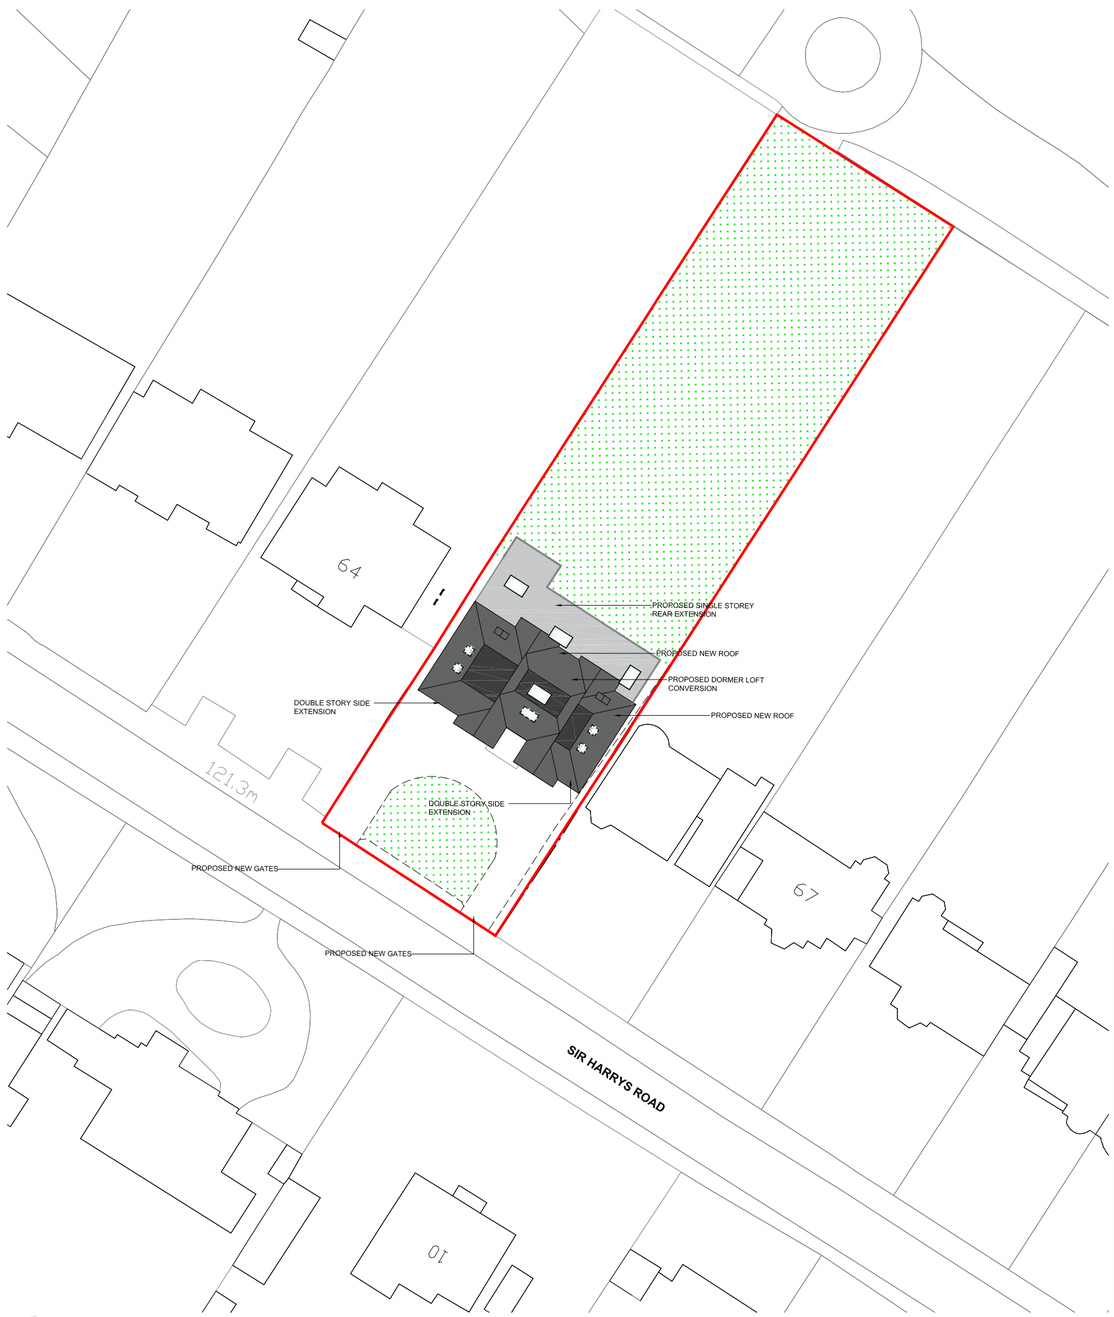

02 Proposed Site Plan
00-099 1:500@A2

Scale 1:500
0 10 20 30

PRITPAL CHANA ARCHITECTS
E: projects@PCarchitects.co.uk
T: 0121 827 5450
W: PCarchitects.co.uk
ARB: 085131K
RIBA: 20015990

1. ALL DIMENSIONS ARE IN MM UNLESS OTHERWISE STATED.
2. DO NOT SCALE DRAWINGS, FIGURED DIMENSIONS TO BE USED ONLY.
3. ALL DETAILS AND DIMENSIONS ARE TO BE CONFIRMED ON SITE. PRIOR TO WORKS COMMENCING OR ANY ORDERING OF MATERIALS.
4. THE CONTRACTOR MUST INFORM THE ARCHITECT OF ANY DISCREPANCIES FOR CLARIFICATION BEFORE PROCEEDING.
5. THE SOLE PURPOSE OF THE DRAWING IS FOR THE ISSUE STATUS ONLY.

CLIENT
Dr. Sabur Malek

PROJECT
65, Sir Harrys Road, B15 2UX

DRAWING TITLE
Site Plan

ISSUE STATUS
PLANNING PERMISSION

SCALE	DRAWN	CHECKED	DATE
1:500 @A2	JAA	PC	04.06.25

JOB NO.	DRG. NO.	REVISION
621	621-00-099	F

NOTES:

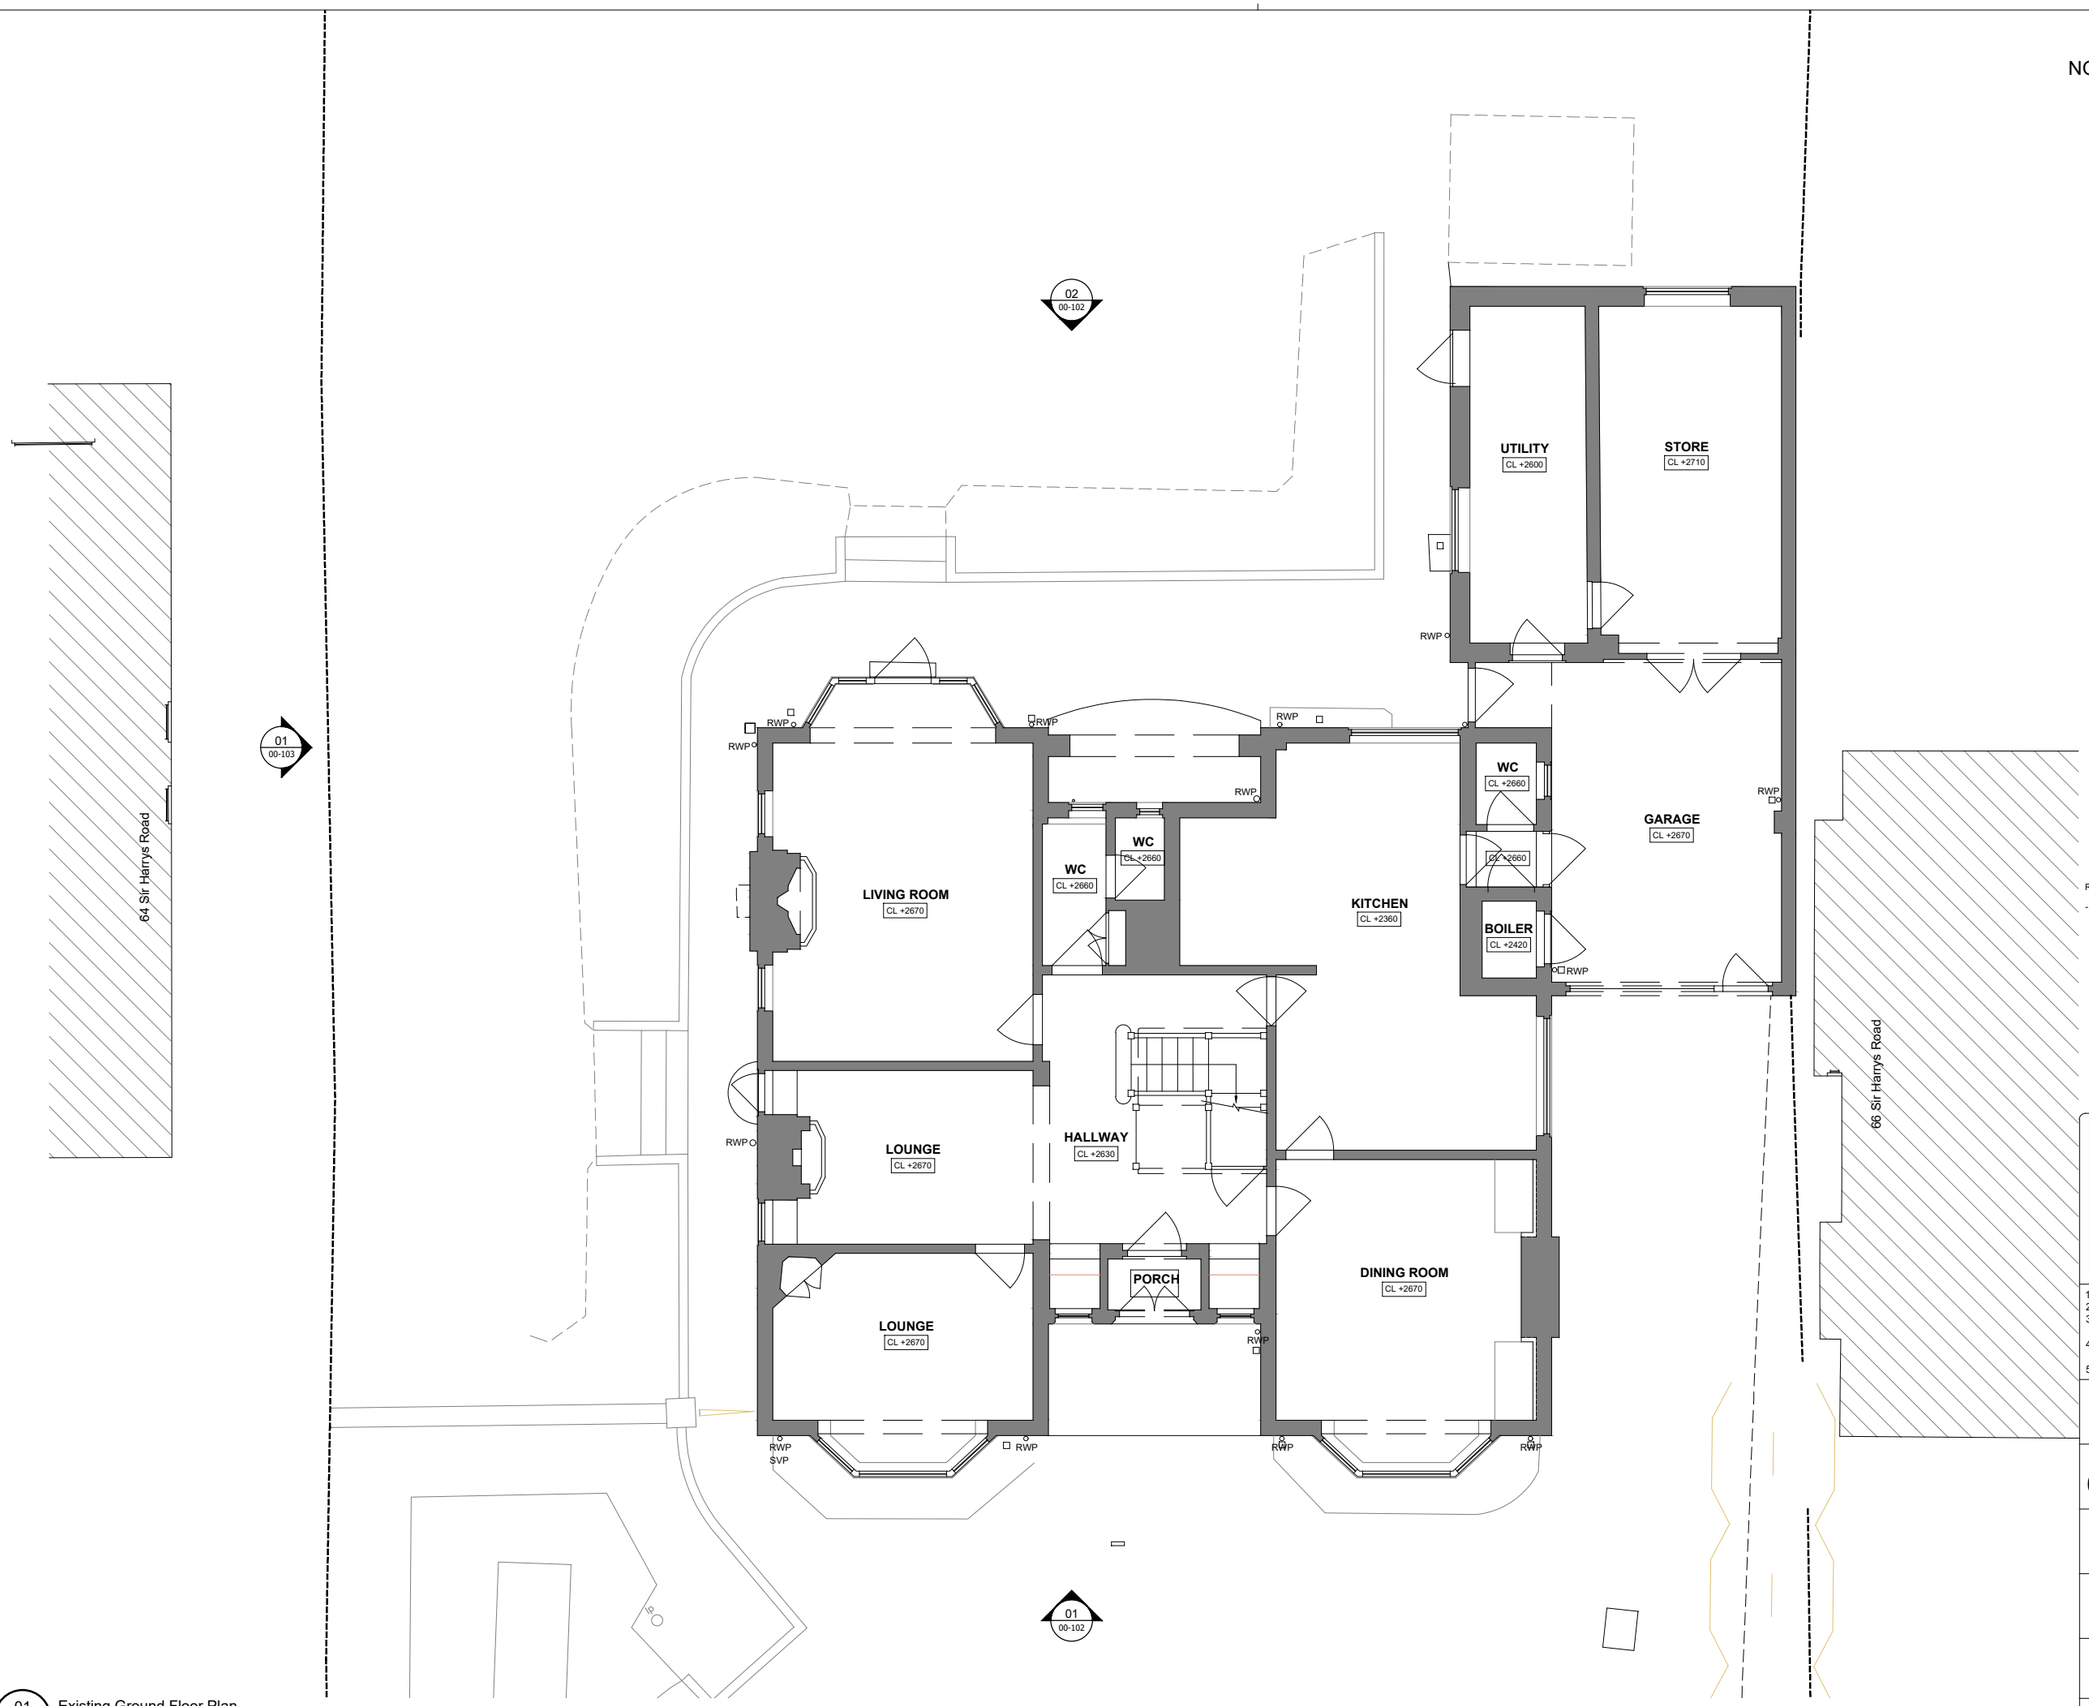

REV	DATE	CHANGES	DRAW
-	xx.xx.24	-	-

SCALE 1:100 *(cm)*
0 100 200

PRITPAL CHANA ARCHITECTS

E: projects@PCarchitects.co.uk
T: 0121 827 5450
W: PCarchitects.co.uk

ARB: 085131K
RIBA: 20015990

1. ALL DIMENSIONS ARE IN MM UNLESS OTHERWISE STATED.
2. DO NOT SCALE DRAWINGS, FIGURED DIMENSIONS TO BE USED ONLY.
3. ALL DETAILS AND DIMENSIONS ARE TO BE CONFIRMED ON SITE, PRIOR TO WORKS COMMENCING OR ANY ORDERING OF MATERIALS.
4. THE CONTRACTOR MUST INFORM THE ARCHITECT OF ANY DISCREPANCIES FOR CLARIFICATION BEFORE PROCEEDING.
5. THE SOLE PURPOSE OF THE DRAWING IS FOR THE ISSUE STATUS ONLY.

CLIENT
Dr. Sabur Malek

PROJECT
65, Sir Harrys Road, B15 2UX

DRAWING TITLE
Existing Ground Floor Plans

ISSUE STATUS
PLANNING PERMISSION

SCALE	DRAWN	CHECKED	DATE
1:100 @A3	SC	PC	20.02.25

JOB NO.	DRG. NO.	REVISION
621	621-00-100	-

01
00-100
Existing Ground Floor Plan
1:100@A3

NOTES:

REV	DATE	CHANGES	DRAW
-	xx.xx.24	-	-

SCALE 1:100 *(cm)*
0 100 200

PRITPAL CHANA ARCHITECTS
E: projects@PCarchitects.co.uk
T: 0121 827 5450
W: PCarchitects.co.uk
ARB: 085131K
RIBA: 20015990

1. ALL DIMENSIONS ARE IN MM UNLESS OTHERWISE STATED.
2. DO NOT SCALE DRAWINGS, FIGURED DIMENSIONS TO BE USED ONLY.
3. ALL DETAILS AND DIMENSIONS ARE TO BE CONFIRMED ON SITE, PRIOR TO WORKS COMMENCING OR ANY ORDERING OF MATERIALS.
4. THE CONTRACTOR MUST INFORM THE ARCHITECT OF ANY DISCREPANCIES FOR CLARIFICATION BEFORE PROCEEDING.
5. THE SOLE PURPOSE OF THE DRAWING IS FOR THE ISSUE STATUS ONLY.

CLIENT
Dr. Sabur Malek

PROJECT
65, Sir Harrys Road, B15 2UX

DRAWING TITLE
Existing First Floor Plans

ISSUE STATUS
PLANNING PERMISSION

SCALE	DRAWN	CHECKED	DATE
1:100 @A3	SC	PC	20.02.25

JOB NO.	DRG. NO.	REVISION
621	621-00-101	-

01 / 00-101 Existing First Floor Plan
1:100@A3

NOTES:

01 Existing South Elevation
00-102 1:100@A3

02 Existing North Elevation
00-102 1:100@A3

REV	DATE	CHANGES	DRAW
-	xx.xx.24	-	-

SCALE 1:100 *(cm)*
0 100 200

PRITPAL CHANA ARCHITECTS

E: projects@PCarchitects.co.uk
T: 0121 827 5450
W: PCarchitects.co.uk

ARB: 085131K
RIBA: 20015990

1. ALL DIMENSIONS ARE IN MM UNLESS OTHERWISE STATED.
2. DO NOT SCALE DRAWINGS, FIGURED DIMENSIONS TO BE USED ONLY.
3. ALL DETAILS AND DIMENSIONS ARE TO BE CONFIRMED ON SITE, PRIOR TO WORKS COMMENCING OR ANY ORDERING OF MATERIALS.
4. THE CONTRACTOR MUST INFORM THE ARCHITECT OF ANY DISCREPANCIES FOR CLARIFICATION BEFORE PROCEEDING.
5. THE SOLE PURPOSE OF THE DRAWING IS FOR THE ISSUE STATUS ONLY.

CLIENT
Dr. Sabur Malek

PROJECT
65, Sir Harrys Road, B15 2UX

DRAWING TITLE
Existing Elevations

ISSUE STATUS
PLANNING PERMISSION

SCALE	DRAWN	CHECKED	DATE
1:100 @A3	SC	PC	20.02.25

JOB NO.	DRG. NO.	REVISION
621	621-00-102	-

NOTES:

01 00-103 Existing West Elevation
West

02 00-103 Existing East Elevation
1:100@A3

REV	DATE	CHANGES	DRAW
-	xx.xx.24	-	-

SCALE 1:100 *(cm)*
0 100 200

PRITPAL CHANA ARCHITECTS
E: projects@PCarchitects.co.uk
T: 0121 827 5450
W: PCarchitects.co.uk
ARB: 085131K
RIBA: 20015990

1. ALL DIMENSIONS ARE IN MM UNLESS OTHERWISE STATED.
2. DO NOT SCALE DRAWINGS, FIGURED DIMENSIONS TO BE USED ONLY.
3. ALL DETAILS AND DIMENSIONS ARE TO BE CONFIRMED ON SITE, PRIOR TO WORKS COMMENCING OR ANY ORDERING OF MATERIALS.
4. THE CONTRACTOR MUST INFORM THE ARCHITECT OF ANY DISCREPANCIES FOR CLARIFICATION BEFORE PROCEEDING.
5. THE SOLE PURPOSE OF THE DRAWING IS FOR THE ISSUE STATUS ONLY.

CLIENT
Dr. Sabur Malek

PROJECT
65, Sir Harrys Road, B15 2UX

DRAWING TITLE
Existing Elevations

ISSUE STATUS
PLANNING PERMISSION

SCALE	DRAWN	CHECKED	DATE
1:100 @A3	SC	PC	20.02.25

JOB NO.	DRG. NO.	REVISION
621	621-00-103	-

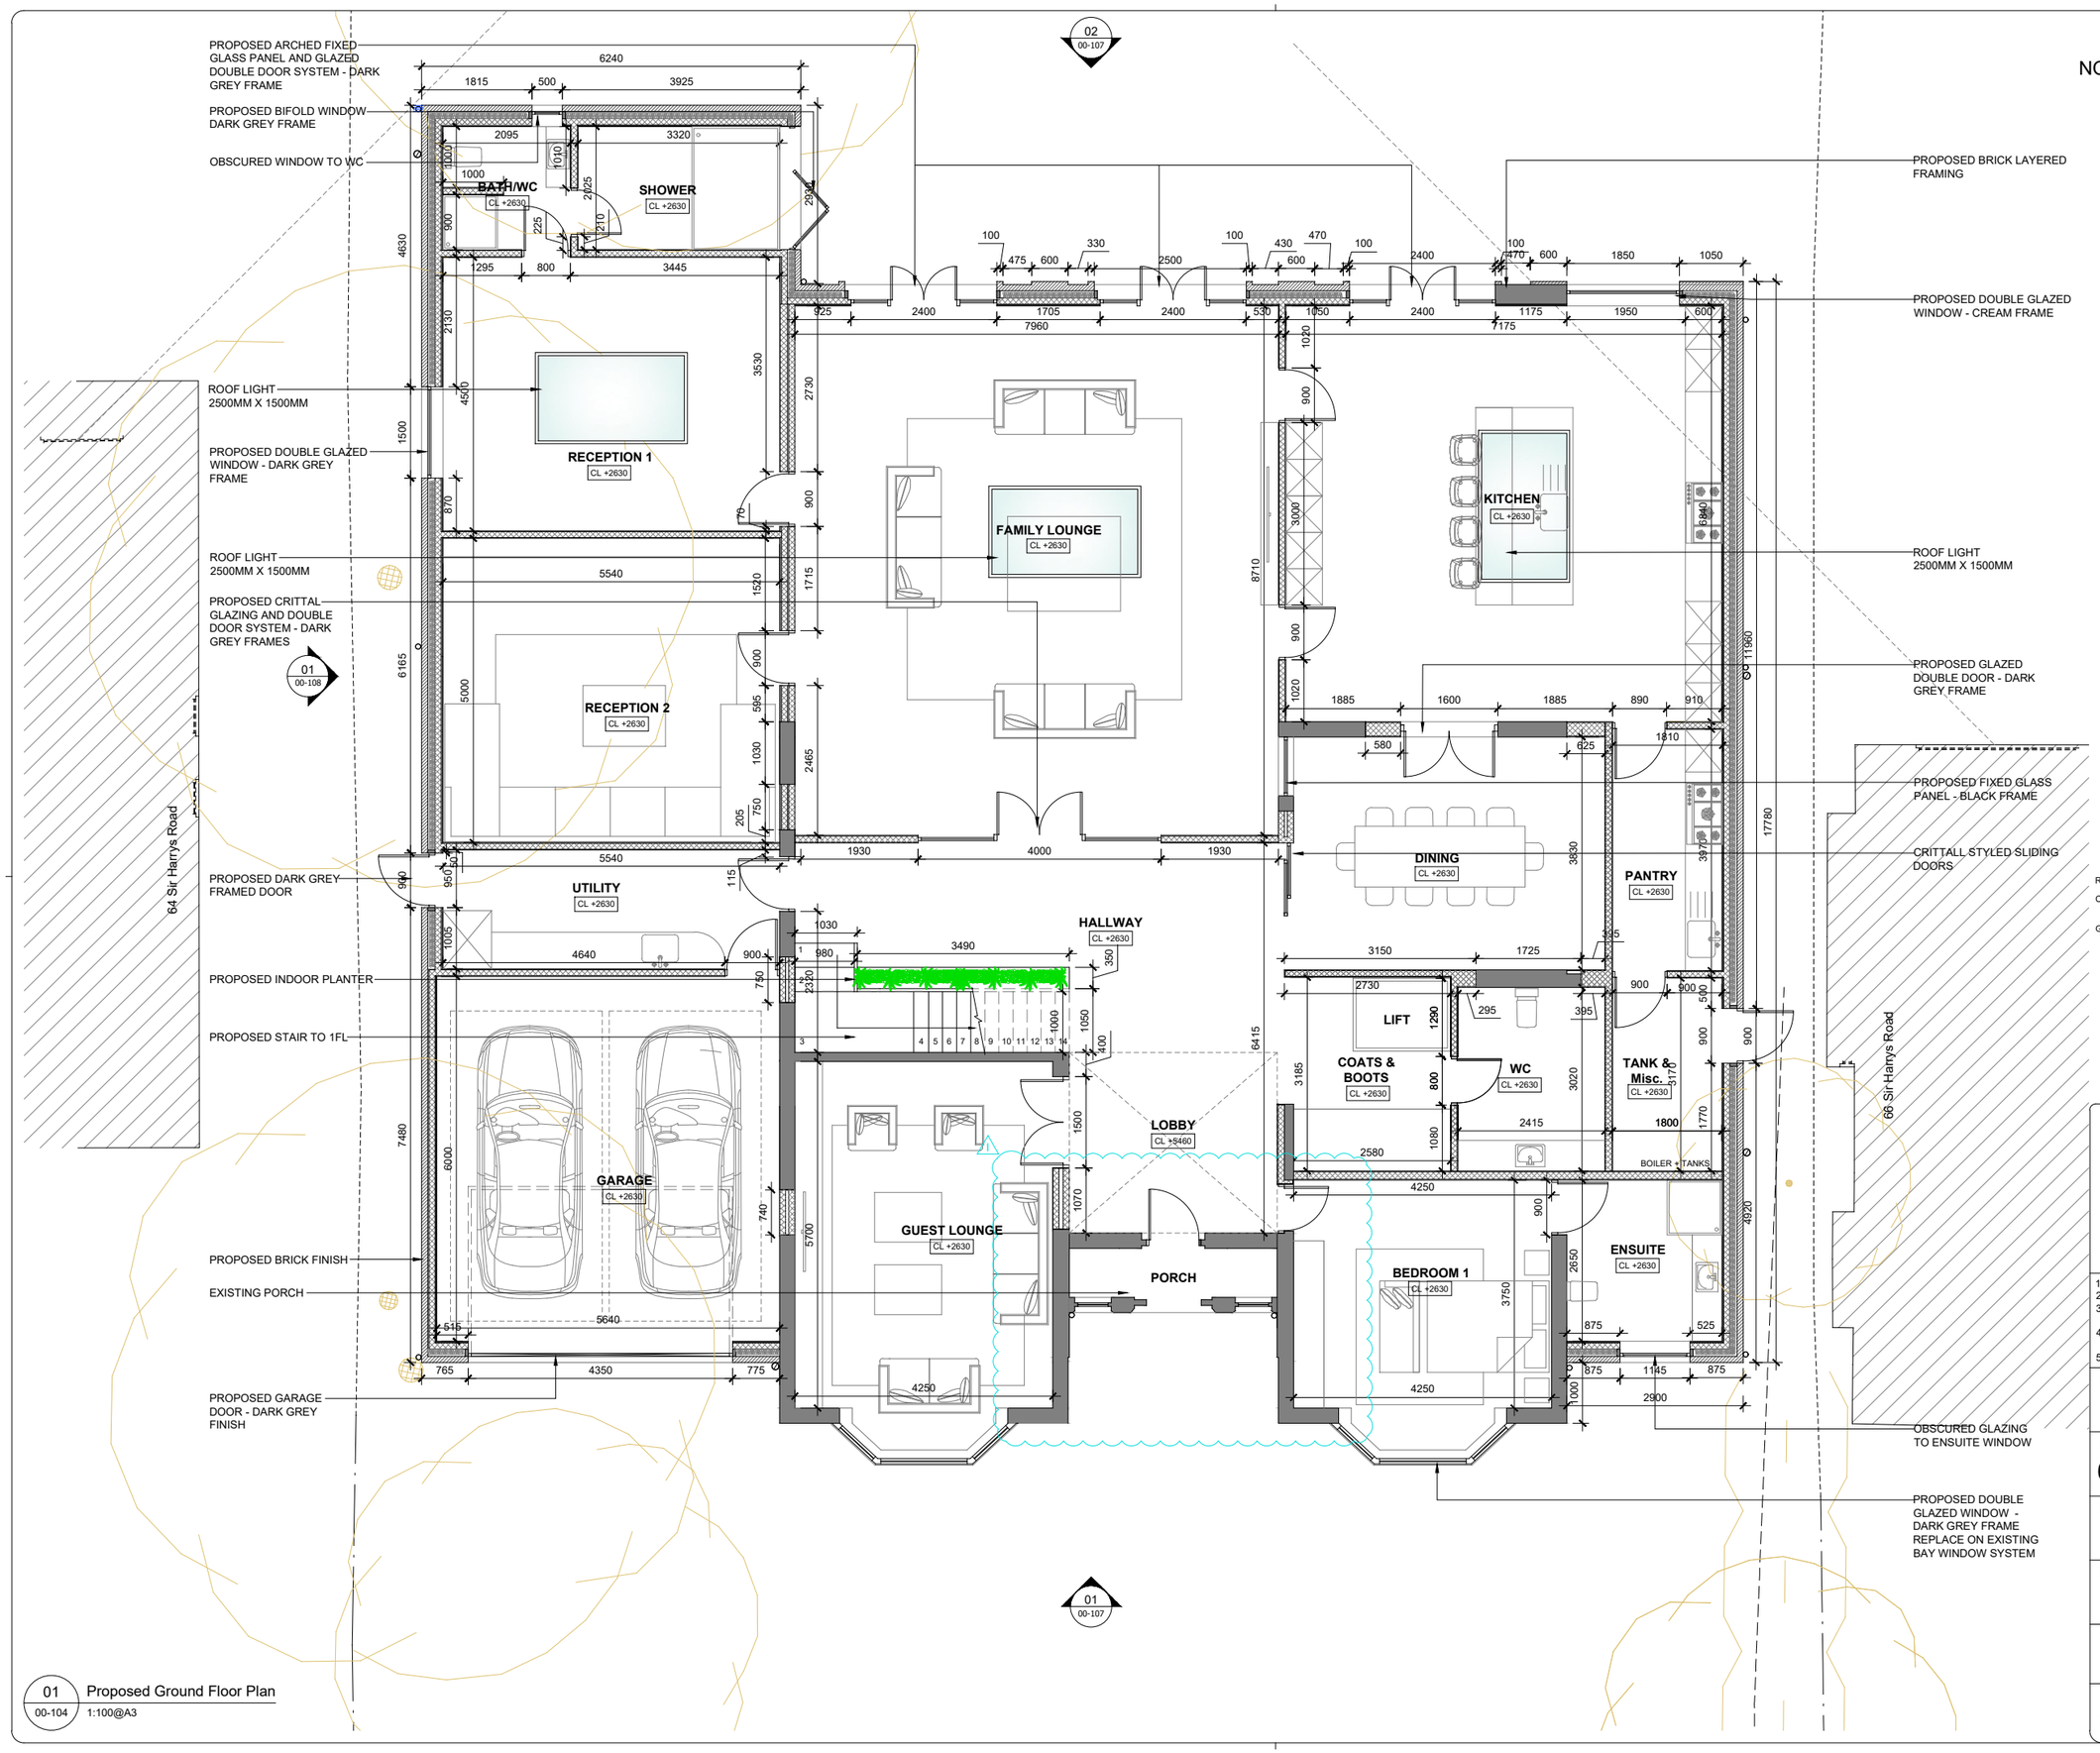

NOTES:

REV	DATE	CHANGES	DRAW
C	30.05.25	Keep existing porch. Maintain permitted boundary.	-
G	28.07.25	Windows removed from pantry, cinema, door added to utility	-

SCALE 1:100 (cm)
0 100 200

PRITPAL CHANA ARCHITECTS
E: projects@PCarchitects.co.uk
T: 0121 827 5450
W: PCarchitects.co.uk
ARB: 085131K
RIBA: 20015990

1. ALL DIMENSIONS ARE IN MM UNLESS OTHERWISE STATED.
2. DO NOT SCALE DRAWINGS, FIGURED DIMENSIONS TO BE USED ONLY.
3. ALL DETAILS AND DIMENSIONS ARE TO BE CONFIRMED ON SITE, PRIOR TO WORKS COMMENCING OR ANY ORDERING OF MATERIALS.
4. THE CONTRACTOR MUST INFORM THE ARCHITECT OF ANY DISCREPANCIES FOR CLARIFICATION BEFORE PROCEEDING.
5. THE SOLE PURPOSE OF THE DRAWING IS FOR THE ISSUE STATUS ONLY.

CLIENT
Dr. Sabur Malek

PROJECT
65, Sir Harrys Road, B15 2UX

DRAWING TITLE
Proposed Ground Floor Plan

ISSUE STATUS
PLANNING PERMISSION

SCALE	DRAWN	CHECKED	DATE
1:100 @A3	JAA	PC	24.10.25

JOB NO.	DRG. NO.	REVISION
621	621-00-104	I

01 / 00-104 Proposed Ground Floor Plan
1:100@A3

NOTES:

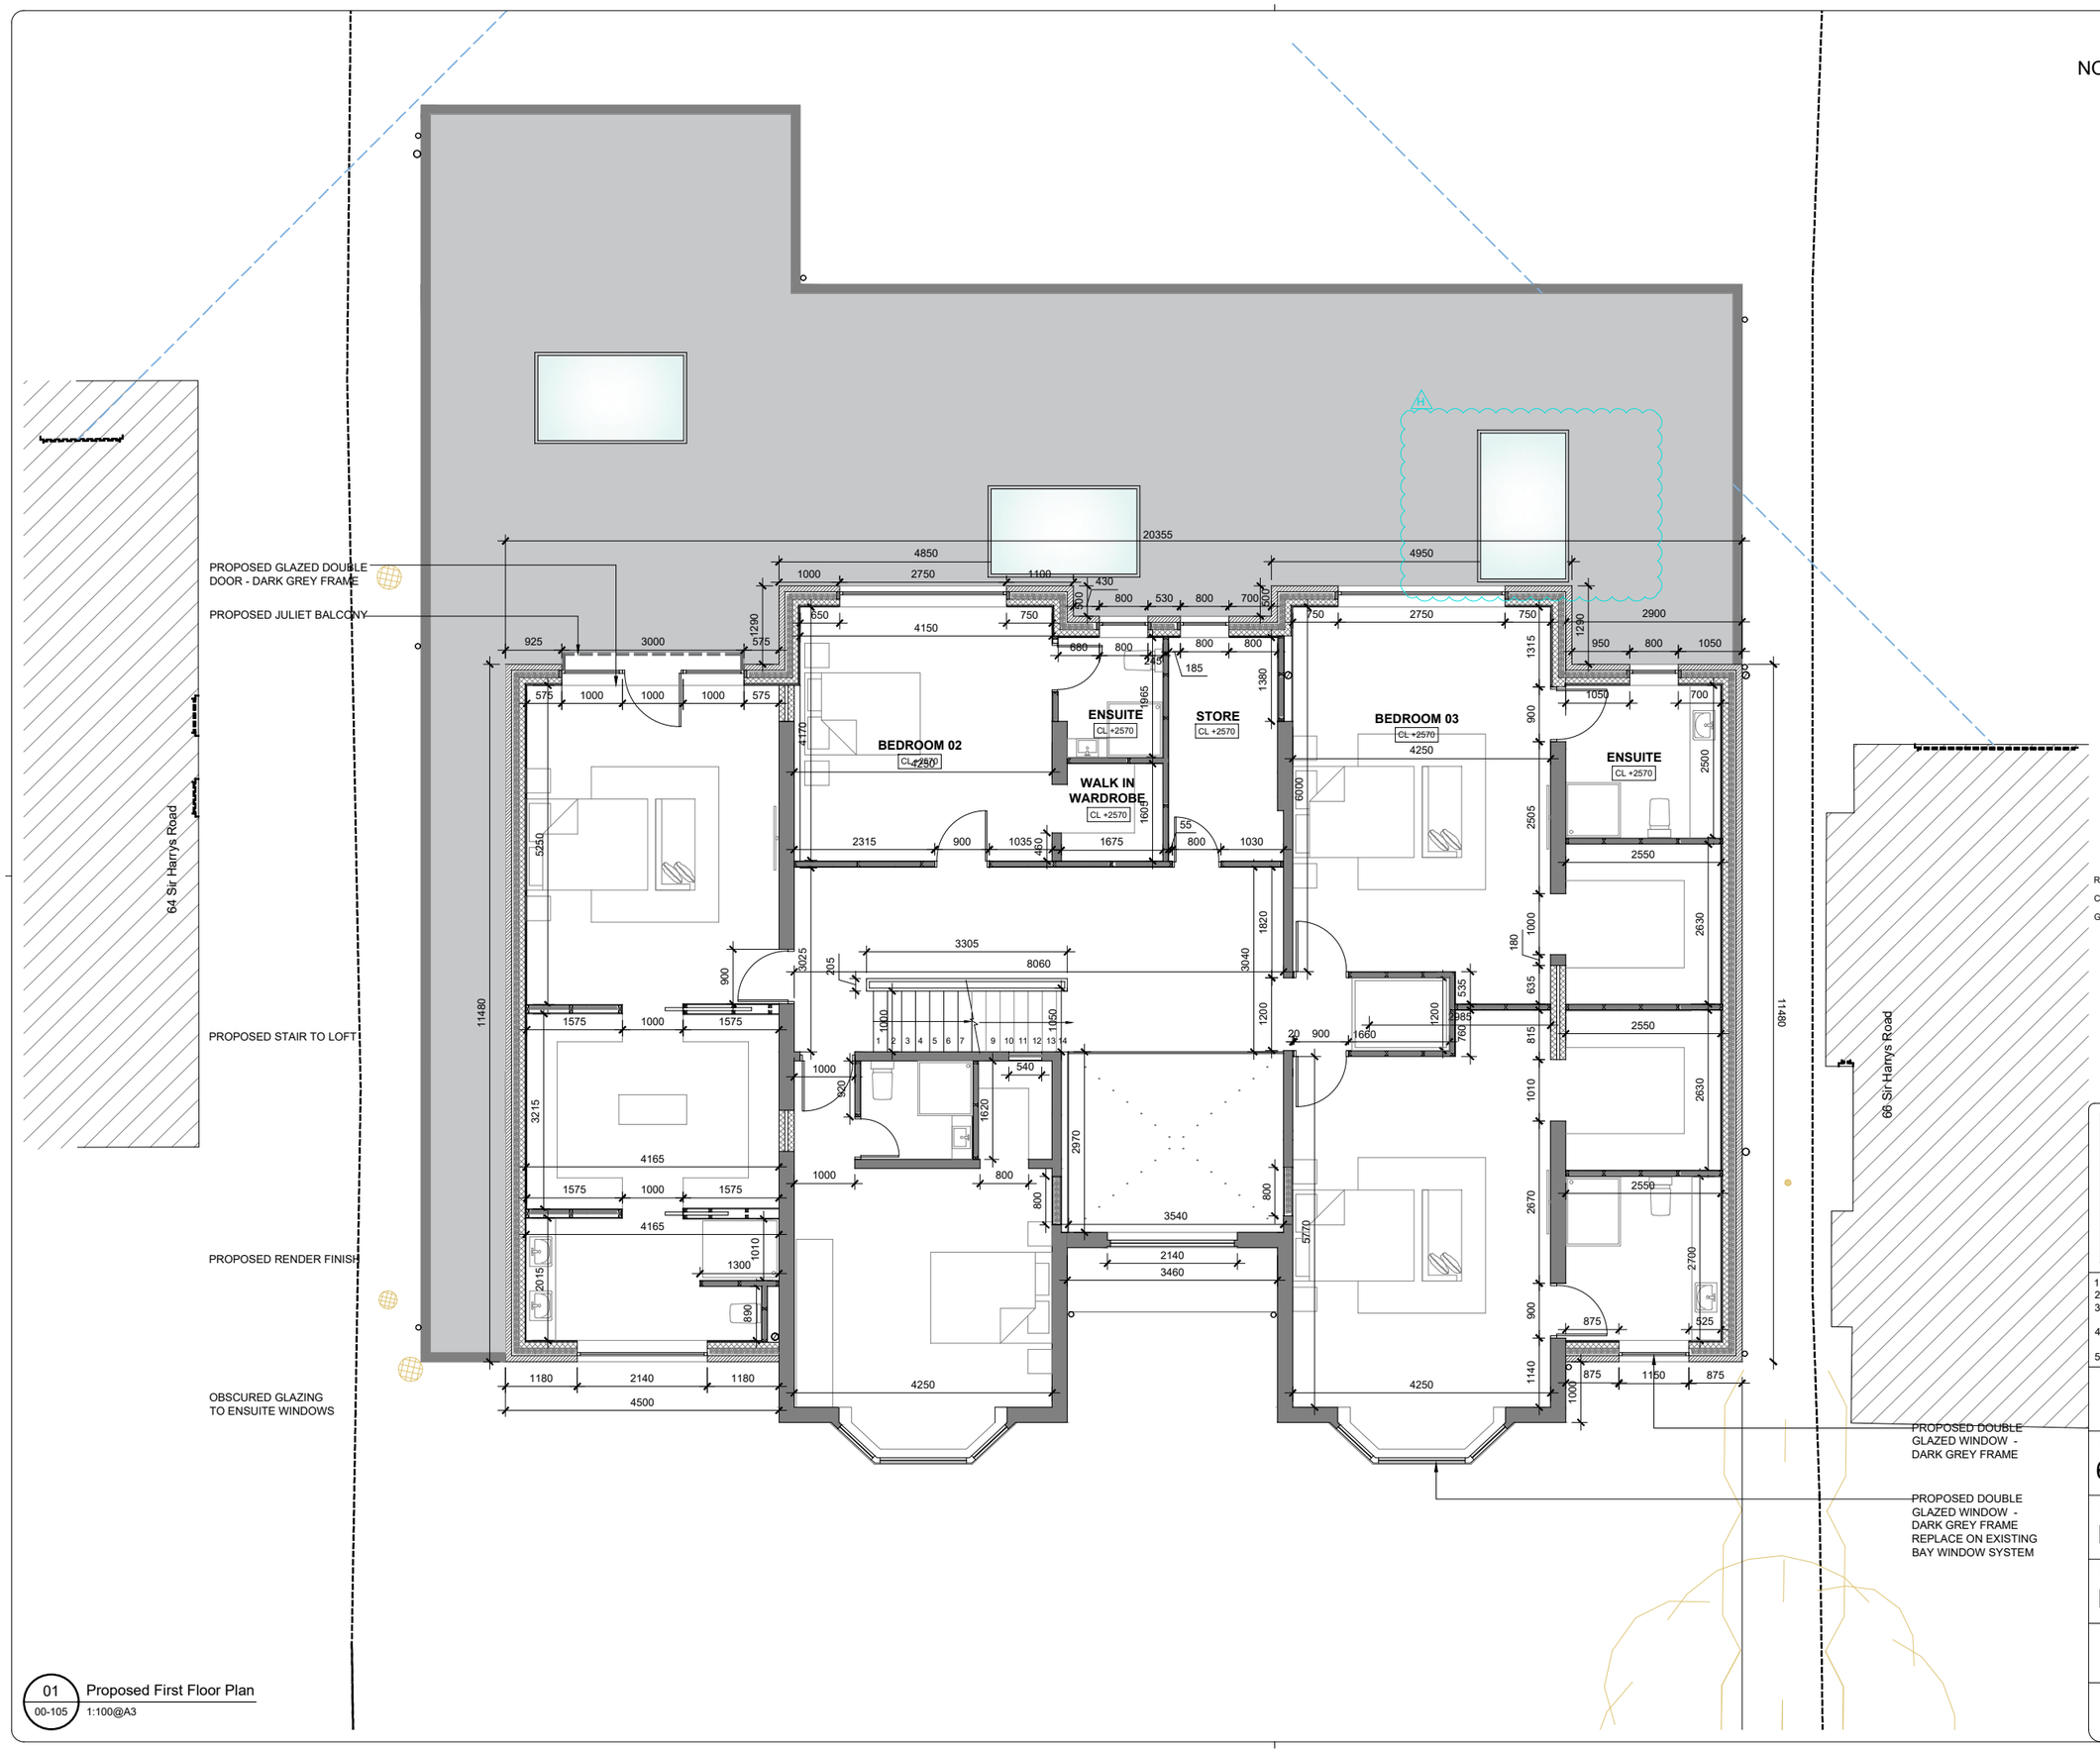

REV	DATE	CHANGES	DRAW
C	30.05.25	Pull back wall inside by 1m	-
G	28.07.25	Windows removed	-

SCALE 1:100 *(cm)*

0 100 200

PRITPAL CHANA ARCHITECTS

E: projects@PCarchitects.co.uk

T: 0121 827 5450

W: PCarchitects.co.uk

ARB: 085131K

RIBA: 20015990

1. ALL DIMENSIONS ARE IN MM UNLESS OTHERWISE STATED.
2. DO NOT SCALE DRAWINGS, FIGURED DIMENSIONS TO BE USED ONLY.
3. ALL DETAILS AND DIMENSIONS ARE TO BE CONFIRMED ON SITE, PRIOR TO WORKS COMMENCING OR ANY ORDERING OF MATERIALS.
4. THE CONTRACTOR MUST INFORM THE ARCHITECT OF ANY DISCREPANCIES FOR CLARIFICATION BEFORE PROCEEDING.
5. THE SOLE PURPOSE OF THE DRAWING IS FOR THE ISSUE STATUS ONLY.

CLIENT
Dr. Sabur Malek

PROJECT
65, Sir Harrys Road, B15 2UX

DRAWING TITLE
Proposed First Floor Plan

ISSUE STATUS
PLANNING PERMISSION

SCALE	DRAWN	CHECKED	DATE
1:100 @A3	JAA	PC	28.07.25

JOB NO.	DRG. NO.	REVISION
621	621-00-105	H

01 Proposed First Floor Plan
00-105 1:100@A3

NOTES:

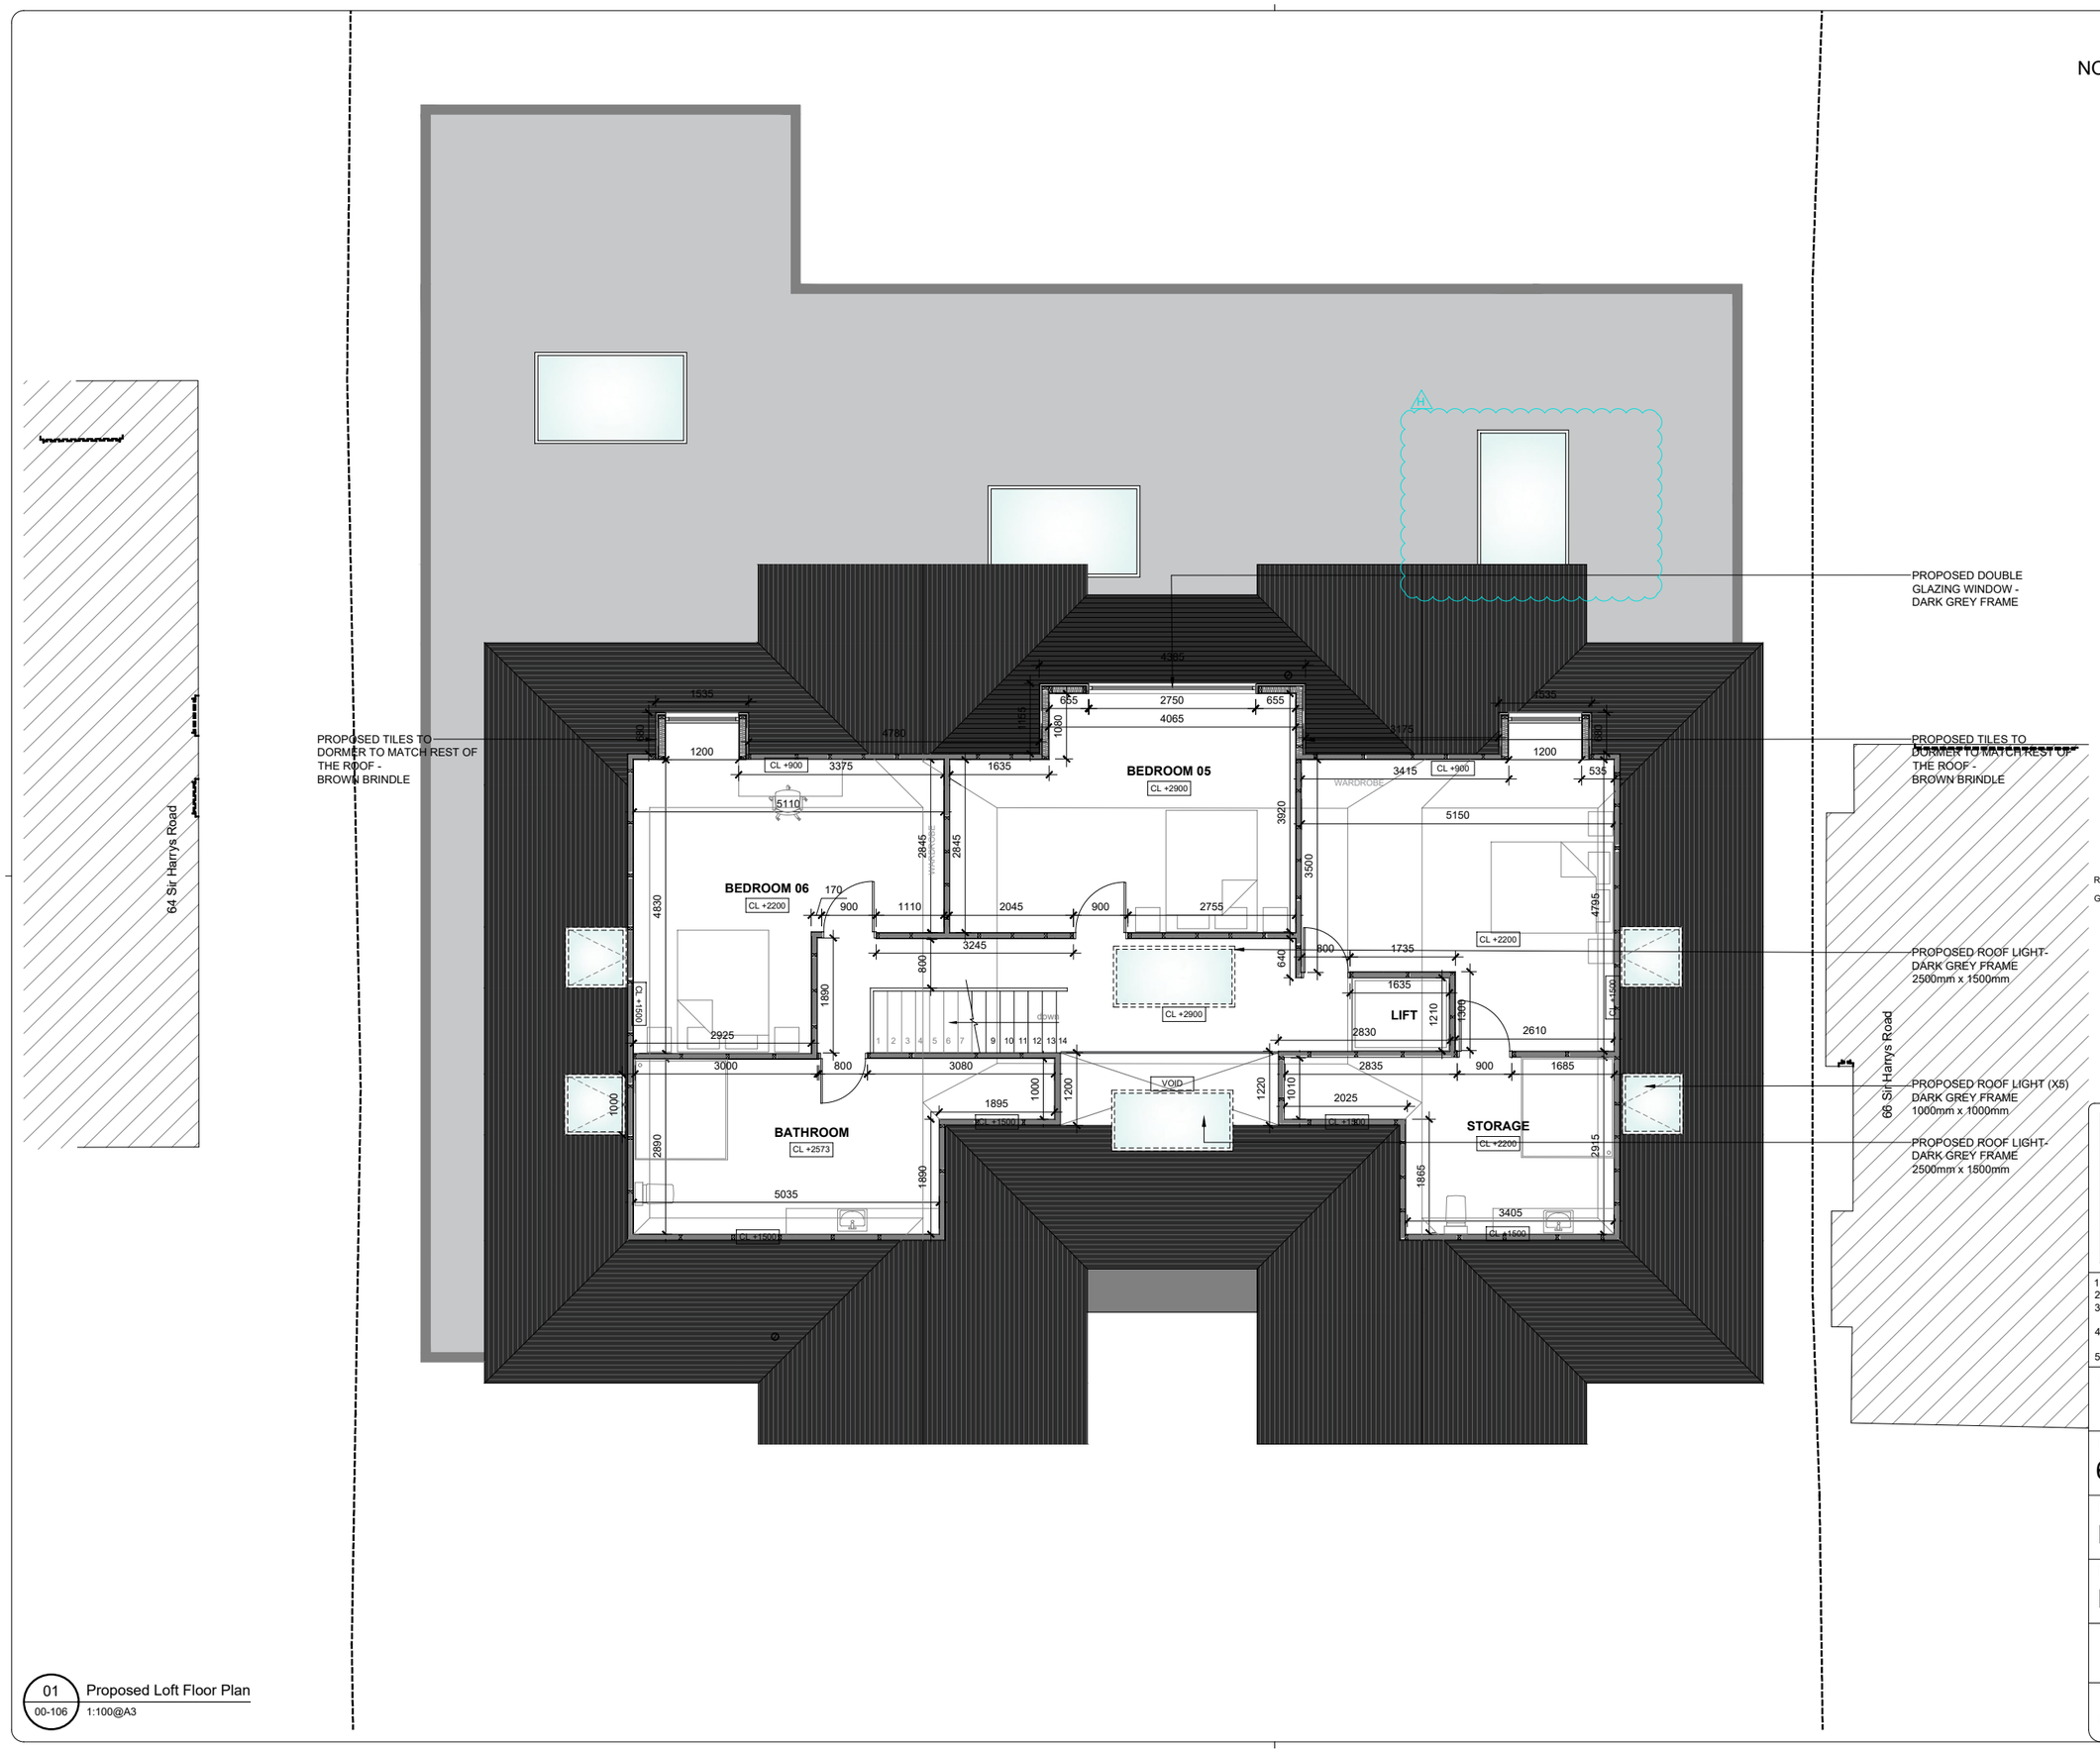

REV	DATE	CHANGES	DRAW
G	28.07.25	Dormer extended to 1200mm	-

SCALE 1:100 *(cm)*

0 100 200

PRITPAL CHANA ARCHITECTS

E: projects@PCarchitects.co.uk

T: 0121 827 5450

W: PCarchitects.co.uk

ARB: 085131K

RIBA: 20015990

1. ALL DIMENSIONS ARE IN MM UNLESS OTHERWISE STATED.
2. DO NOT SCALE DRAWINGS, FIGURED DIMENSIONS TO BE USED ONLY.
3. ALL DETAILS AND DIMENSIONS ARE TO BE CONFIRMED ON SITE, PRIOR TO WORKS COMMENCING OR ANY ORDERING OF MATERIALS.
4. THE CONTRACTOR MUST INFORM THE ARCHITECT OF ANY DISCREPANCIES FOR CLARIFICATION BEFORE PROCEEDING.
5. THE SOLE PURPOSE OF THE DRAWING IS FOR THE ISSUE STATUS ONLY.

CLIENT

Dr. Sabur Malek

PROJECT

65, Sir Harrys Road, B15 2UX

DRAWING TITLE

Proposed Loft Floor Plan

ISSUE STATUS

PLANNING PERMISSION

SCALE	DRAWN	CHECKED	DATE
1:100 @A3	JAA	PC	28.07.25

JOB NO.	DRG. NO.	REVISION
621	621-00-106	H

01 / 00-106 Proposed Loft Floor Plan

1:100@A3

NOTES:

01 00-107 Proposed South Elevation
1:100@A3

REV	DATE	CHANGES	DRAW
C	30.05.25	Replace Front Porch to existing	-
D	04.06.25	Increase Gable roof height	
G	28.07.25	Dormer width altered	
H	08.08.25	Width corrected	

02 00-107 Proposed North Elevation
1:100@A3

SCALE 1:100 *(cm)*
0 100 200

PRITPAL CHANA ARCHITECTS
E: projects@PCarchitects.co.uk
T: 0121 827 5450
W: PCarchitects.co.uk
ARB: 085131K
RIBA: 20015990

1. ALL DIMENSIONS ARE IN MM UNLESS OTHERWISE STATED.
2. DO NOT SCALE DRAWINGS, FIGURED DIMENSIONS TO BE USED ONLY.
3. ALL DETAILS AND DIMENSIONS ARE TO BE CONFIRMED ON SITE, PRIOR TO WORKS COMMENCING OR ANY ORDERING OF MATERIALS.
4. THE CONTRACTOR MUST INFORM THE ARCHITECT OF ANY DISCREPANCIES FOR CLARIFICATION BEFORE PROCEEDING.
5. THE SOLE PURPOSE OF THE DRAWING IS FOR THE ISSUE STATUS ONLY.

CLIENT
Dr. Sabur Malek

PROJECT
65, Sir Harrys Road, B15 2UX

DRAWING TITLE
Proposed Elevations

ISSUE STATUS
PLANNING PERMISSION

SCALE	DRAWN	CHECKED	DATE
1:100 @A3	JAA	PC	28.07.25

JOB NO.	DRG. NO.	REVISION
621	621-00-107	H

NOTES:

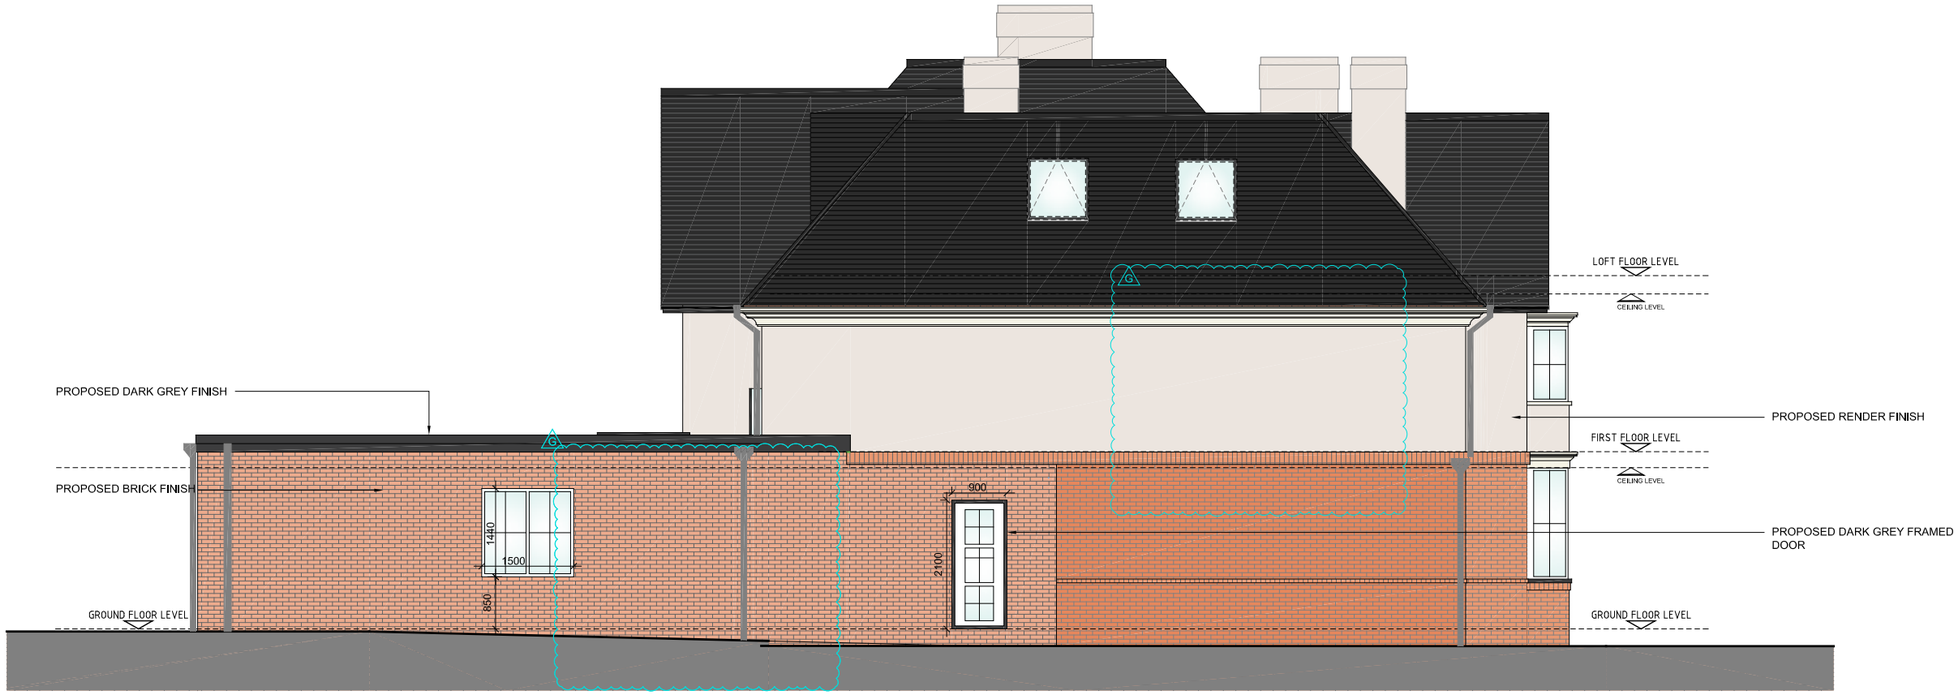

01 / 00-108 Proposed West Elevation
1:100@A3

02 / 00-108 Proposed East Elevation
1:100@A3

REV	DATE	CHANGES	DRAW
G	28.07.25	Windows for walk in wardrobe and cinema room removed	-

SCALE 1:100 (cm)
0 100 200

PRITPAL CHANA ARCHITECTS
E: projects@PCarchitects.co.uk
T: 0121 827 5450
W: PCarchitects.co.uk
ARB: 085131K
RIBA: 20015990

1. ALL DIMENSIONS ARE IN MM UNLESS OTHERWISE STATED.
2. DO NOT SCALE DRAWINGS, FIGURED DIMENSIONS TO BE USED ONLY.
3. ALL DETAILS AND DIMENSIONS ARE TO BE CONFIRMED ON SITE, PRIOR TO WORKS COMMENCING OR ANY ORDERING OF MATERIALS.
4. THE CONTRACTOR MUST INFORM THE ARCHITECT OF ANY DISCREPANCIES FOR CLARIFICATION BEFORE PROCEEDING.
5. THE SOLE PURPOSE OF THE DRAWING IS FOR THE ISSUE STATUS ONLY.

CLIENT
Dr. Sabur Malek

PROJECT
65, Sir Harrys Road, B15 2UX

DRAWING TITLE
Proposed Elevations

ISSUE STATUS
PLANNING PERMISSION

SCALE	DRAWN	CHECKED	DATE
1:100 @A3	JAA	PC	04.06.25

JOB NO.	DRG. NO.	REVISION
621	621-00-108	G