All dimensions and levels to be checked on site by contractor prior to commencement of work.

EXISTING SOUTH ELEVATION

EXISTING WEST ELEVATION

EXISTING NORTH ELEVATION

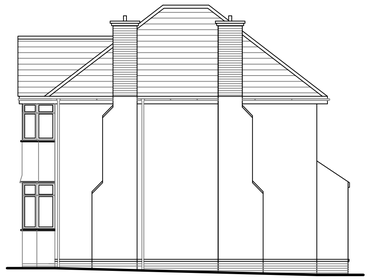

EXISTING EAST ELEVATION

SCALE BAR 1:500

SCALE BAR 1:1250

SCALE BAR 1:100

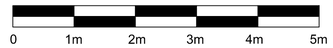

SCALE BAR 1:50

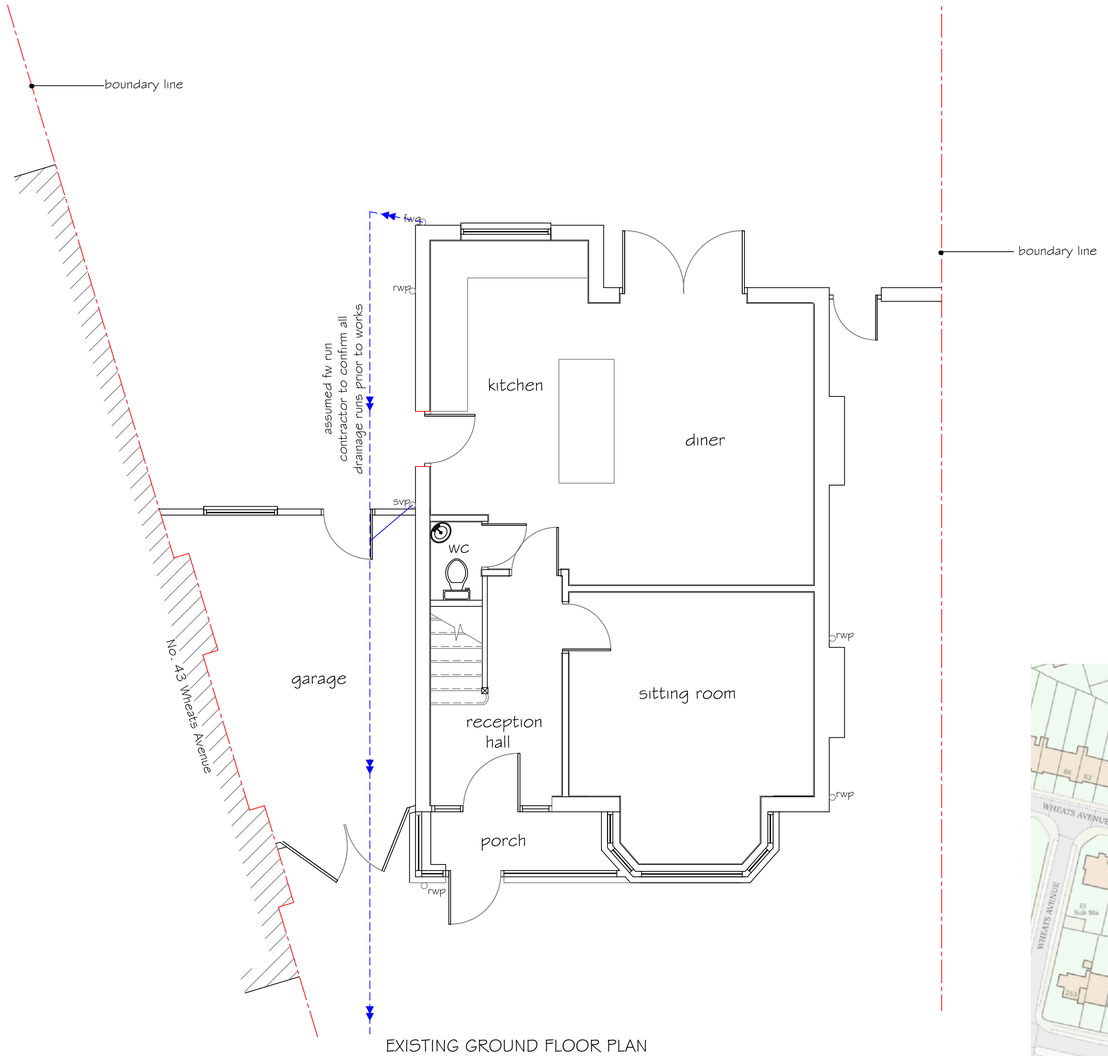

EXISTING GROUND FLOOR PLAN

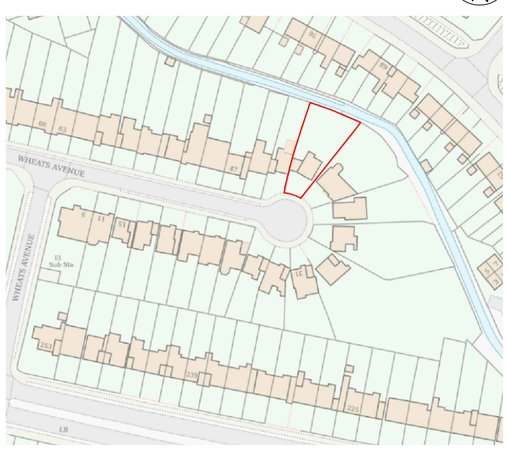

LOCATION PLAN @ 1:1250

PROPOSED SITE PLAN @ 1:500

Job:
Single storey side extension and rear extension:

41 Wheats Avenue
Harborne
Birmingham
B17 0RH

Title:
Existing Ground Floor Plan, Elevations and Site Plans

PURVIS DAWES & PARTNERS LTD
BUILDING DESIGN AND PROJECT MANAGEMENT
178a Lower High Street Stourbridge. DY8 1TG
Tel: 01384905058 email: enquiries@pdp-ltd.co.uk

Scale: 1:50 & 1:100 on A1

Date: September 2025

Drawing No.
2521–01
Rev B