All dimensions and levels to be checked on site by contractor prior to commencement of work.

PROPOSED SOUTH ELEVATION

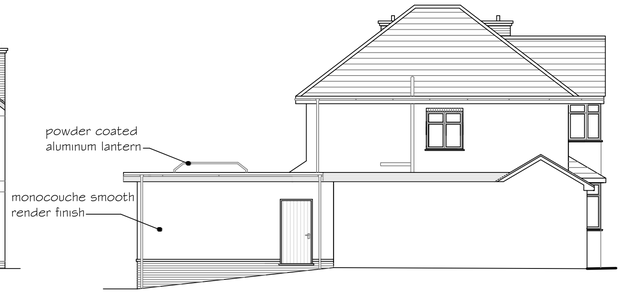

PROPOSED WEST ELEVATION

PROPOSED NORTH ELEVATION

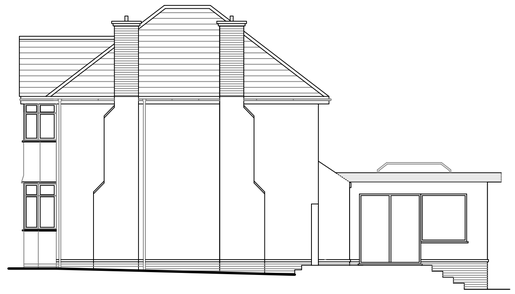

PROPOSED EAST ELEVATION

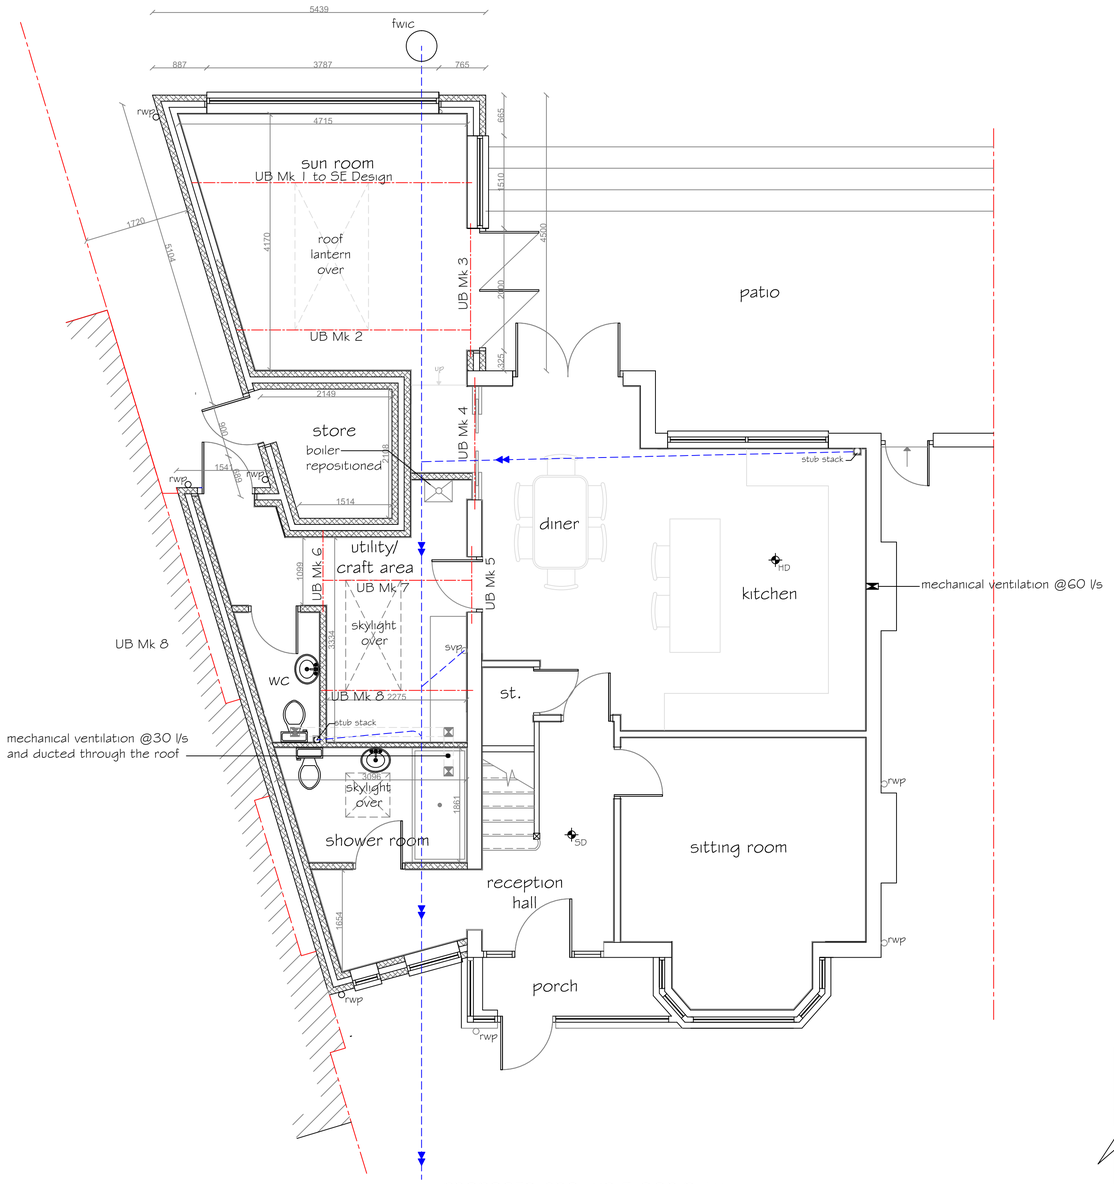

PROPOSED GROUND FLOOR PLAN

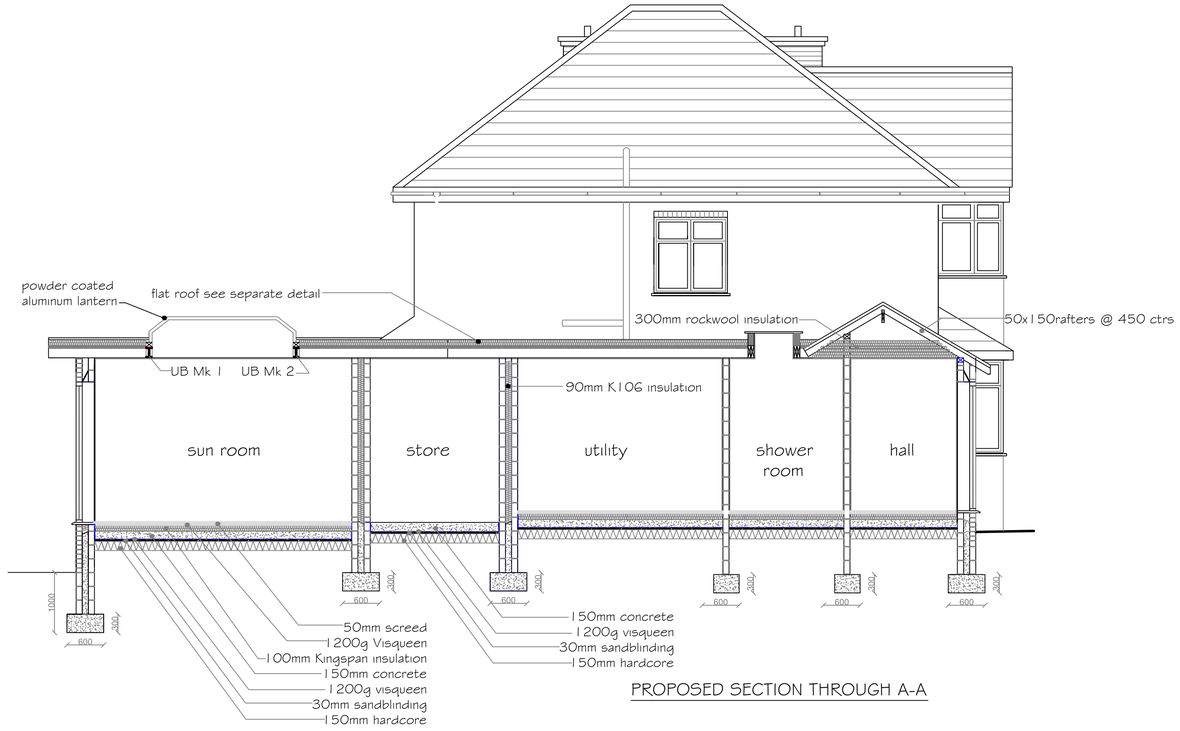

PROPOSED SECTION THROUGH A-A

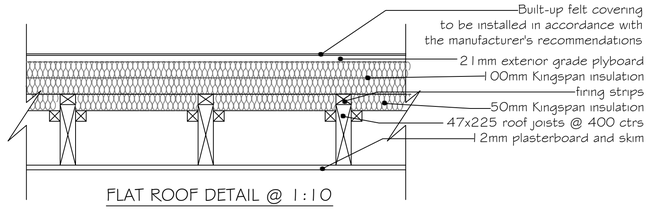

FLAT ROOF DETAIL @ 1:10

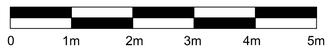

SCALE BAR 1:50

SCALE BAR 1:100

Job:
Single storey side extension and rear extension:

41 Wheats Avenue
Harborne
Birmingham
B17 0RH

Scale: 1:50 & 1:100 on A1

Date: October 2025

PURVIS DAWES & PARTNERS LTD
BUILDING DESIGN AND PROJECT MANAGEMENT
178a Lower High Street Stourbridge. DY8 1TG
Tel: 01384905058 email: enquiries@pdp-ltd.co.uk

Drawing No.
2521-02
Rev E

Title:
Proposed Ground Floor Plan, Elevations And Section Details