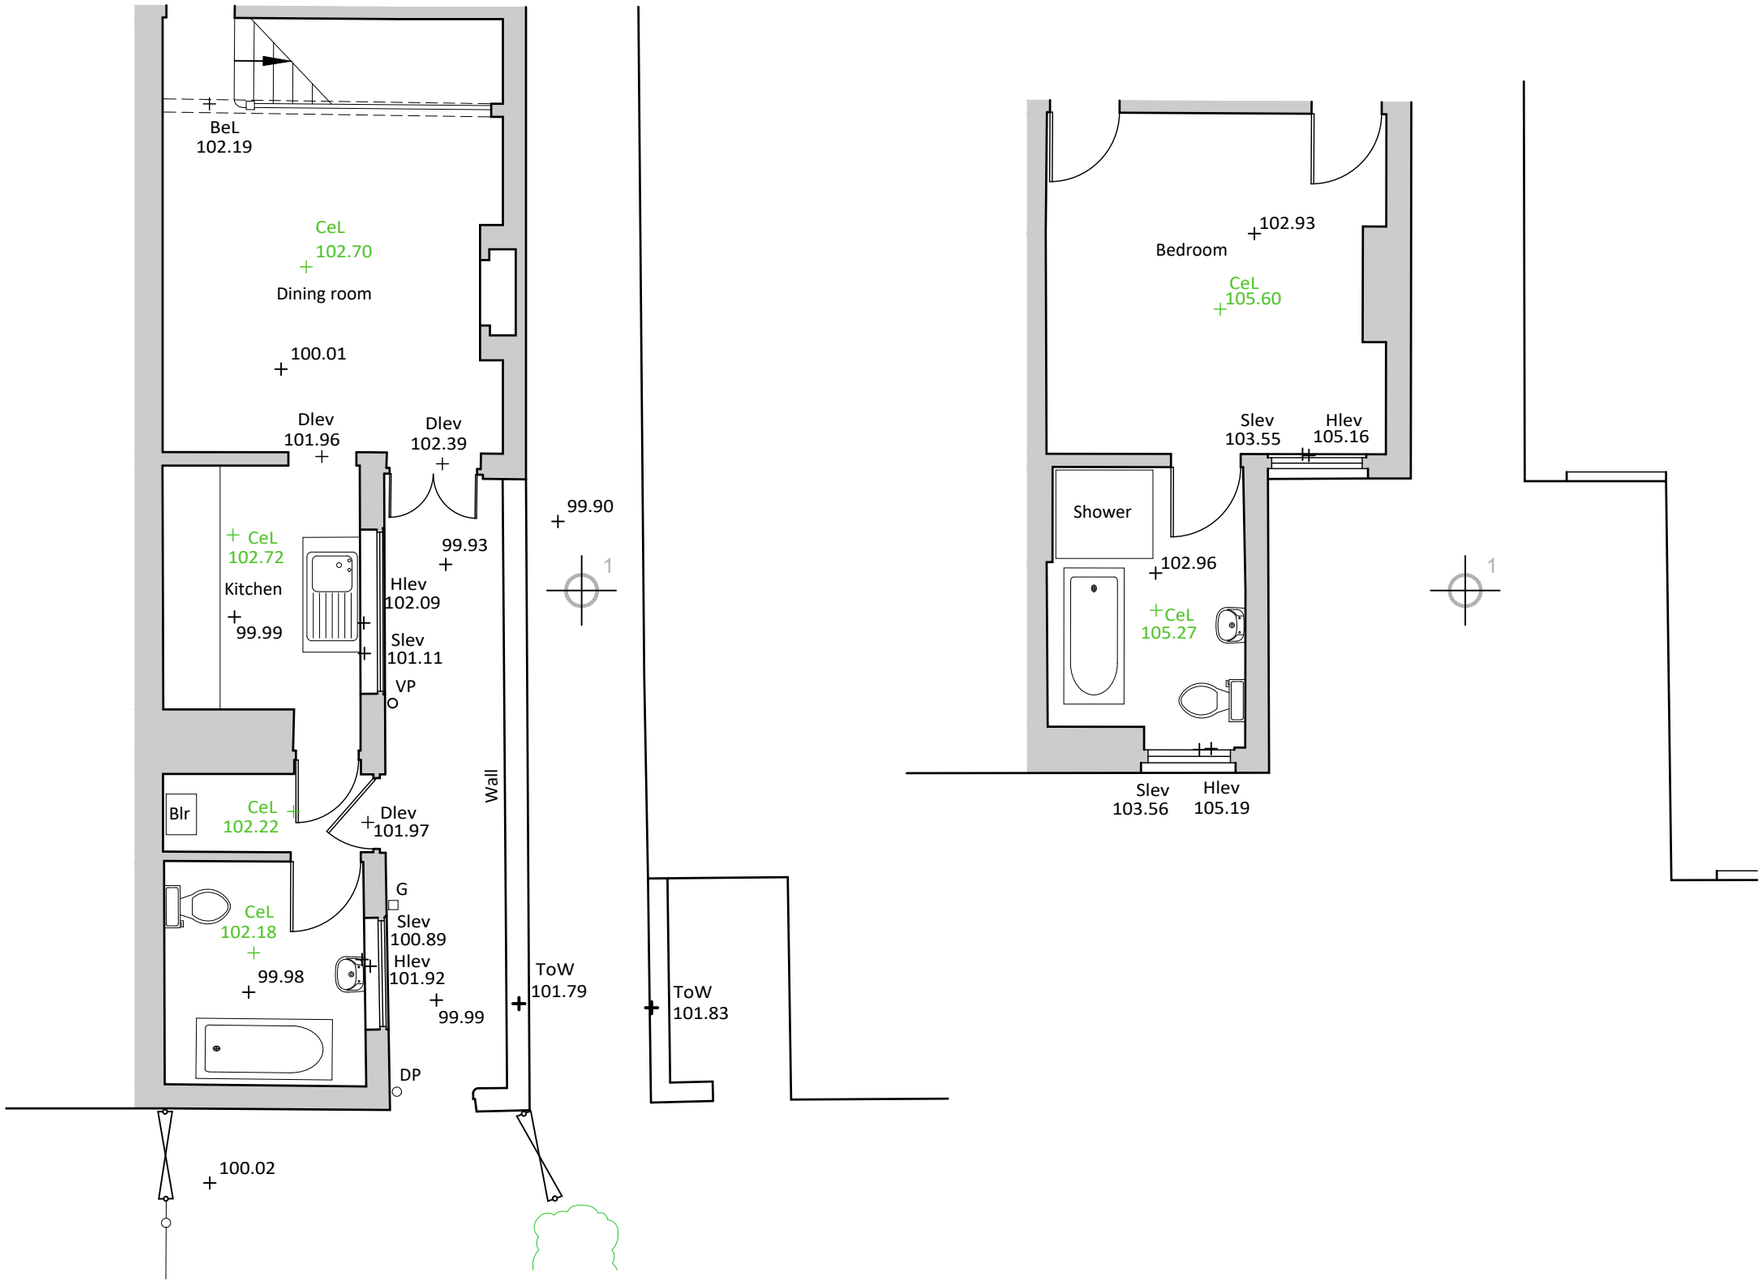

Existing Part Ground & First Floor Plans

1:50 Scale

0 0.5 1 2 3 m

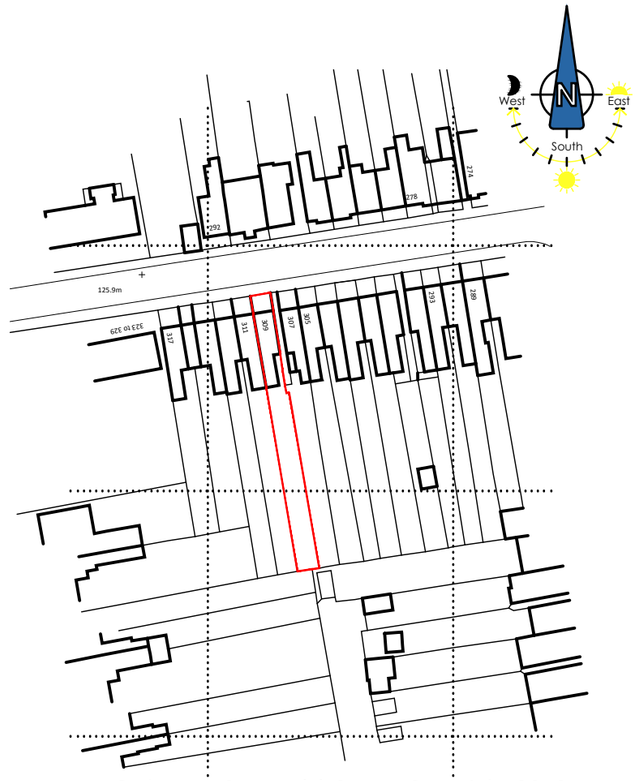

Ordnance Survey (c) Crown Copyright 2013.
All rights reserved. Licence number 100022432

Location Plan

1:1250 Scale

0 5 10 25 50 75 100m

The copyright of this drawing is vested in S&S Architecture (UK) Ltd & is not to be reproduced, copied, or used for any other purpose than intended without the prior written consent of S&S Architecture (UK) Ltd.
The electronic version of this drawing is to scale on an A3 sheet. Each scale stated refers to the drawing above it, so if anyone prints this drawing please ensure that it has been printed at the correct size (A3) & not 'Scaled to Fit'. Scale bars have been provided for the purpose to check this, so if the bar scales do not scale correctly the drawing sheet has not been printed correctly.
Preferably use figured dimensions (if shown) and report any discrepancies to S&S Architecture (UK) Ltd immediately.

S&S Architecture (UK) Ltd

Architecture

T : 0121 382 5959
M : 07989 648867
E : stephen@sandsarchitecture.co.uk

www.sandsarchitecture.co.uk

Client	Mr Sidwell - 309 Highbridge Road, Sutton Coldfield, West Midlands. B73 5RB
Dwg	Existing Part Ground & First Floor Plans.
Scale	1:50
Date	Dec. 2024
Dwg No.	2025.013-01

Existing Side Elevation

1:50 Scale

0 0.5 1 2 3 m

Datum 98.00m

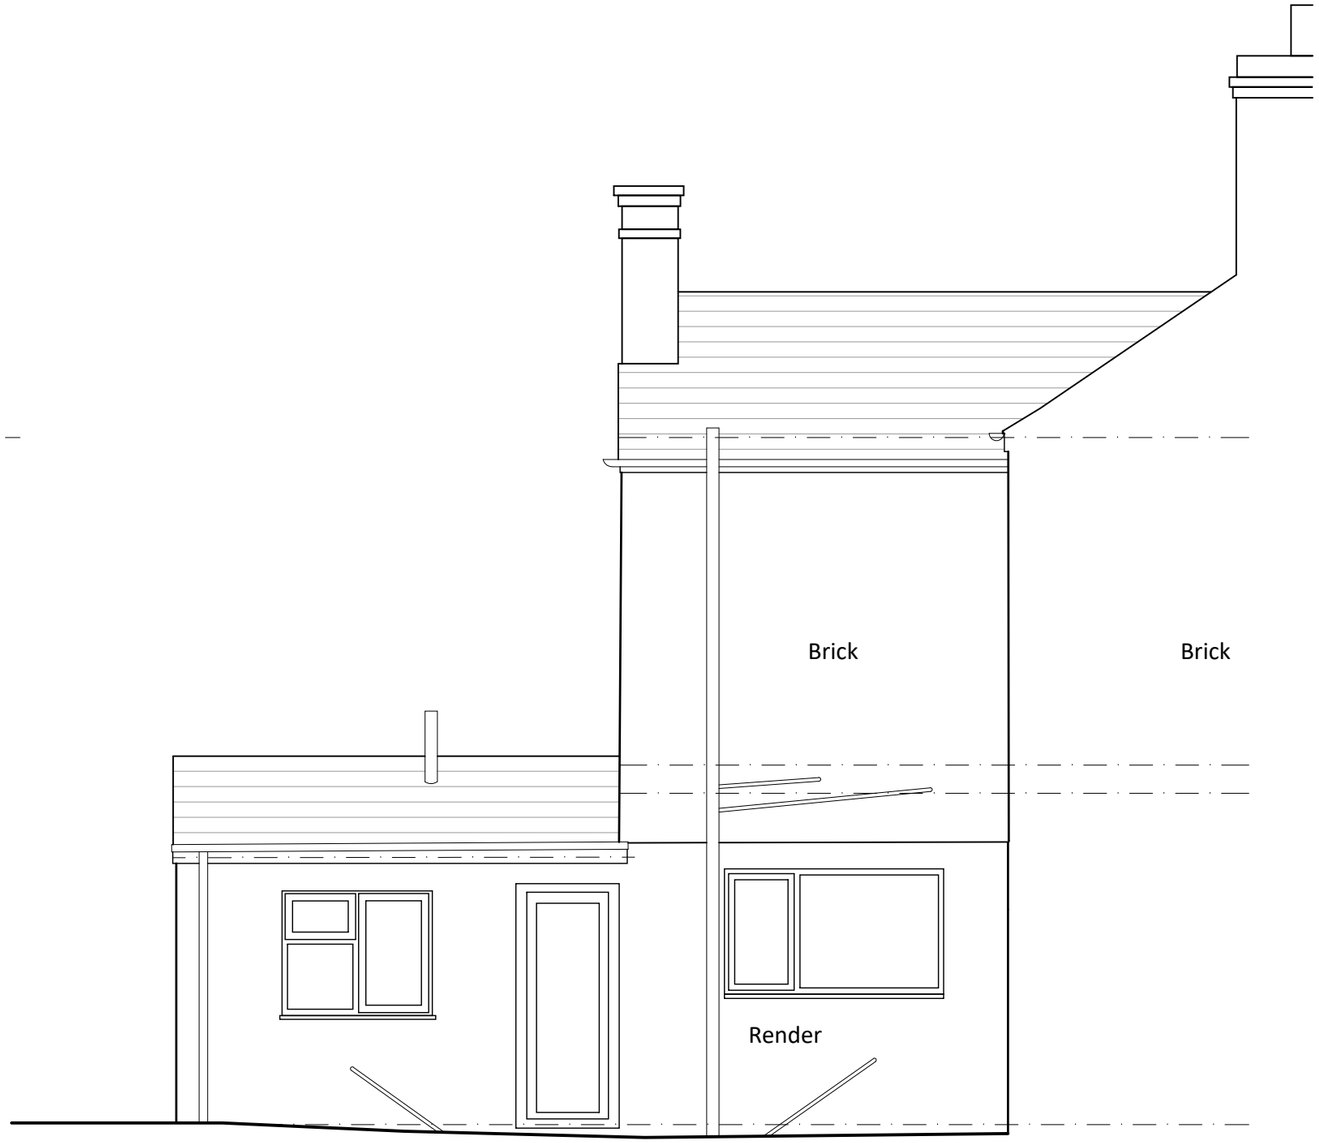

Existing Rear Elevation

1:50 Scale

0 0.5 1 2 3 m

Datum 98.00m

The copyright of this drawing is vested in S&S Architecture (UK) Ltd & is not to be reproduced, copied, or used for any other purpose than intended without the prior written consent of S&S Architecture (UK) Ltd.
The electronic version of this drawing is to scale on an A3 sheet. Each scale stated refers to the drawing above it, so if anyone prints this drawing please ensure that it has been printed at the correct size (A3) & not 'Scaled to Fit'. Scale bars have been provided for the purpose to check this, so if the bar scales do not scale correctly the drawing sheet has not been printed correctly.
Preferably use figured dimensions (if shown) and report any discrepancies to S&S Architecture (UK) Ltd immediately.

S&S Architecture (UK) Ltd

Architecture

T : 0121 382 5959

M : 07989 648867

E : stephen@sandsarchitecture.co.uk

www.sandsarchitecture.co.uk

Client	Mr Sidwell - 309 Highbridge Road, Sutton Coldfield, West Midlands. B73 5RB
Dwg	Existing Elevations.
Scale	1:50
Date	Dec. 2024
Dwg No.	2025.013-02

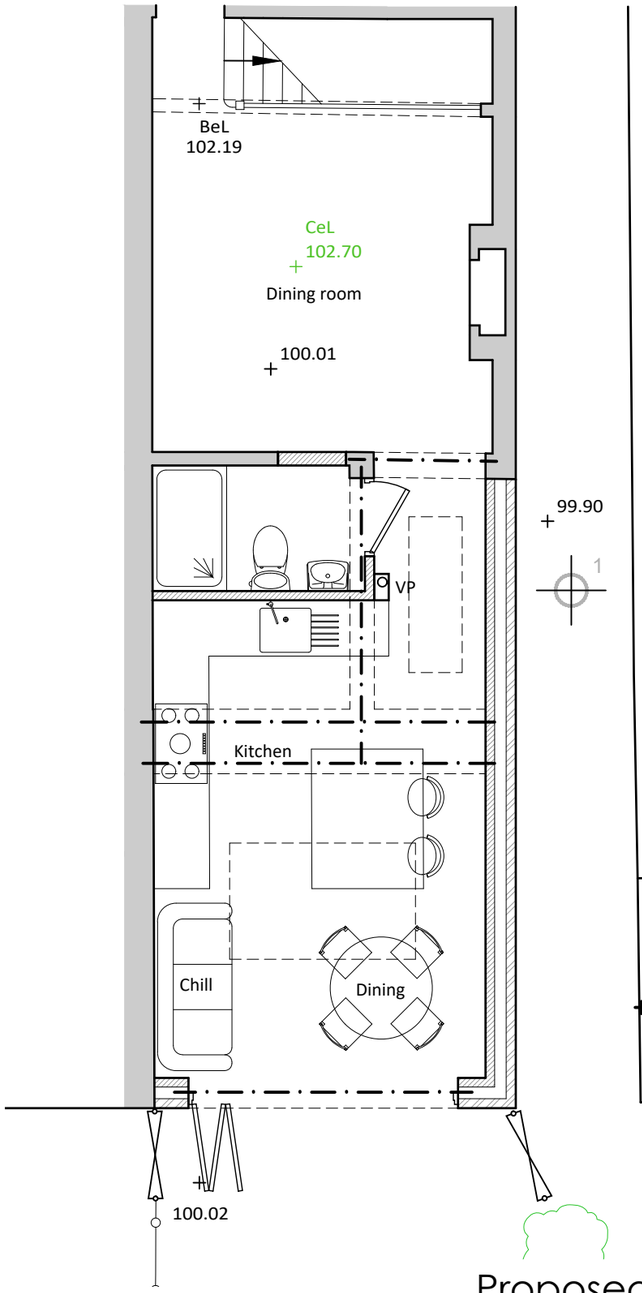

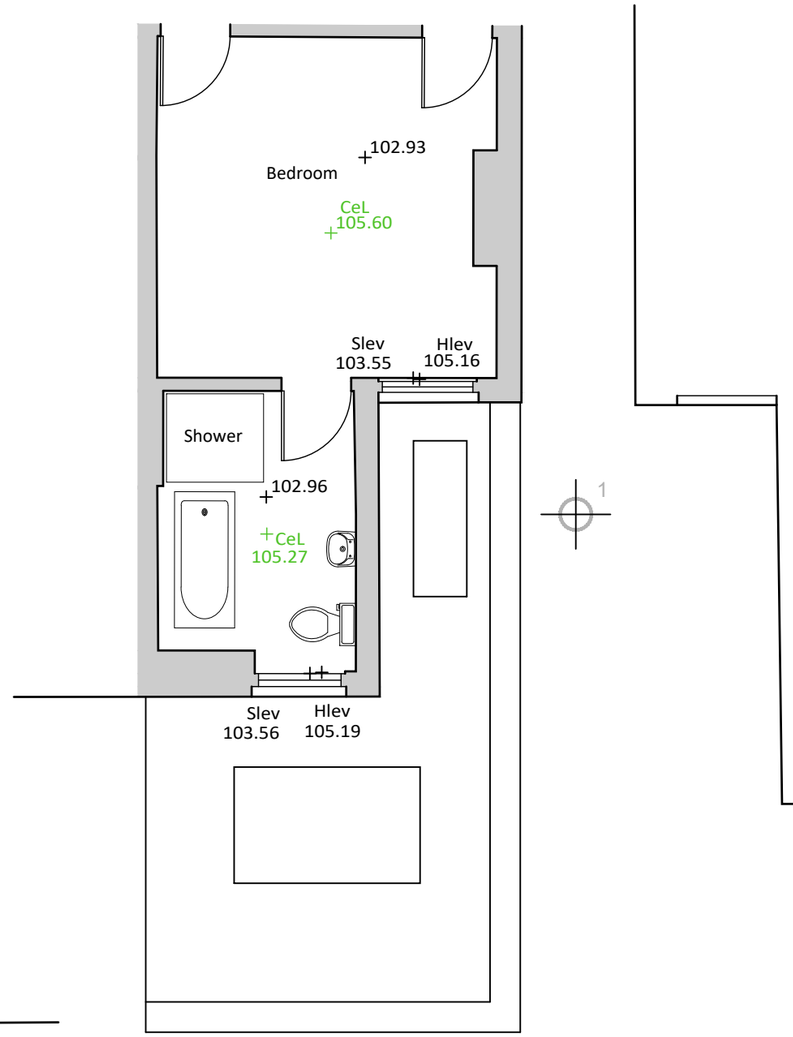

Proposed Part Ground & First Floor Plans

1:50 Scale

0 0.5 1 2 3 m

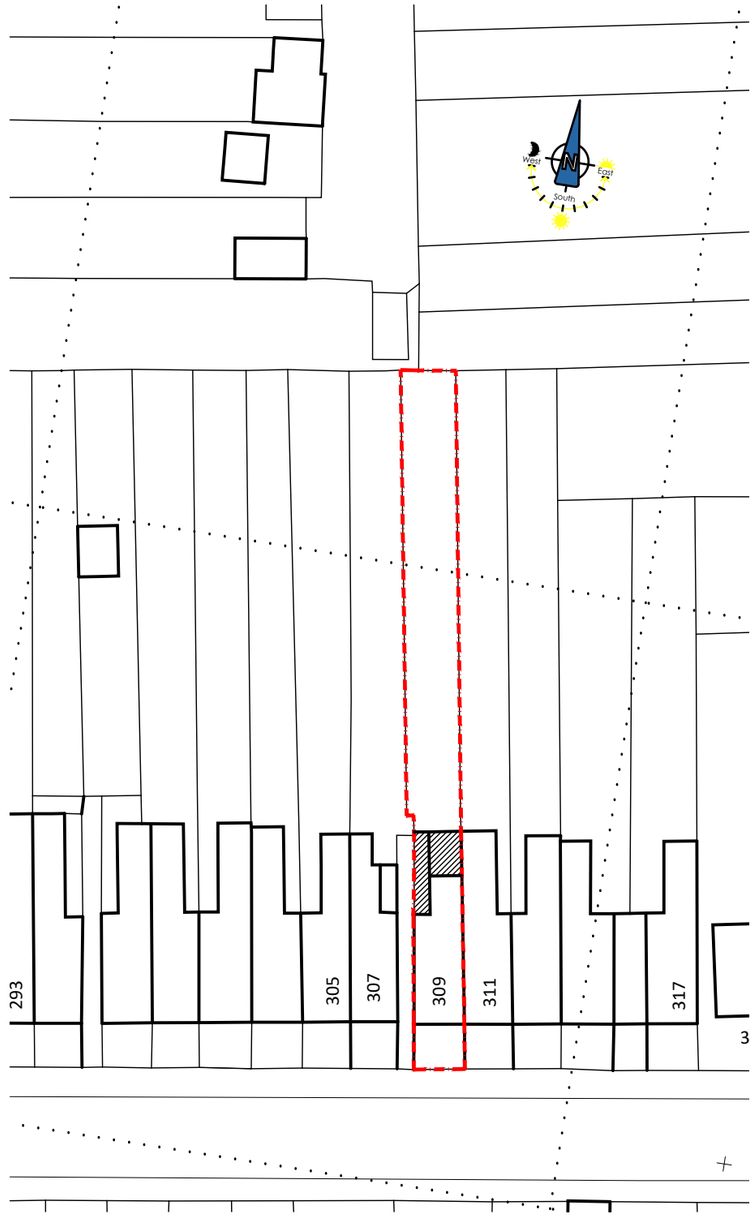

Block Plan

1:500 Scale

0 2 5 10 20 40 m

The copyright of this drawing is vested in S&S Architecture (UK) Ltd & is not to be reproduced, copied, or used for any other purpose than intended without the prior written consent of S&S Architecture (UK) Ltd.
The electronic version of this drawing is to scale on an A3 sheet. Each scale stated refers to the drawing above it, so if anyone prints this drawing please ensure that it has been printed at the correct size (A3) & not 'Scaled to Fit'. Scale bars have been provided for the purpose to check this, so if the bar scales do not scale correctly the drawing sheet has not been printed correctly.
Preferably use figured dimensions (if shown) and report any discrepancies to S&S Architecture (UK) Ltd immediately.

S&S Architecture (UK) Ltd
Architecture
T : 0121 382 5959
M : 07989 648867
E : stephen@sandsarchitecture.co.uk
www.sandsarchitecture.co.uk

Client	Mr Sidwell - 309 Highbridge Road, Sutton Coldfield, West Midlands. B73 5RB
Dwg	Proposed Part Ground & First Floor Plans.
Scale	1:50
Date	Dec. 2024
Dwg No.	2025.013-03

Proposed Rear Elevation

1:50 Scale

0 0.5 1 2 3 m

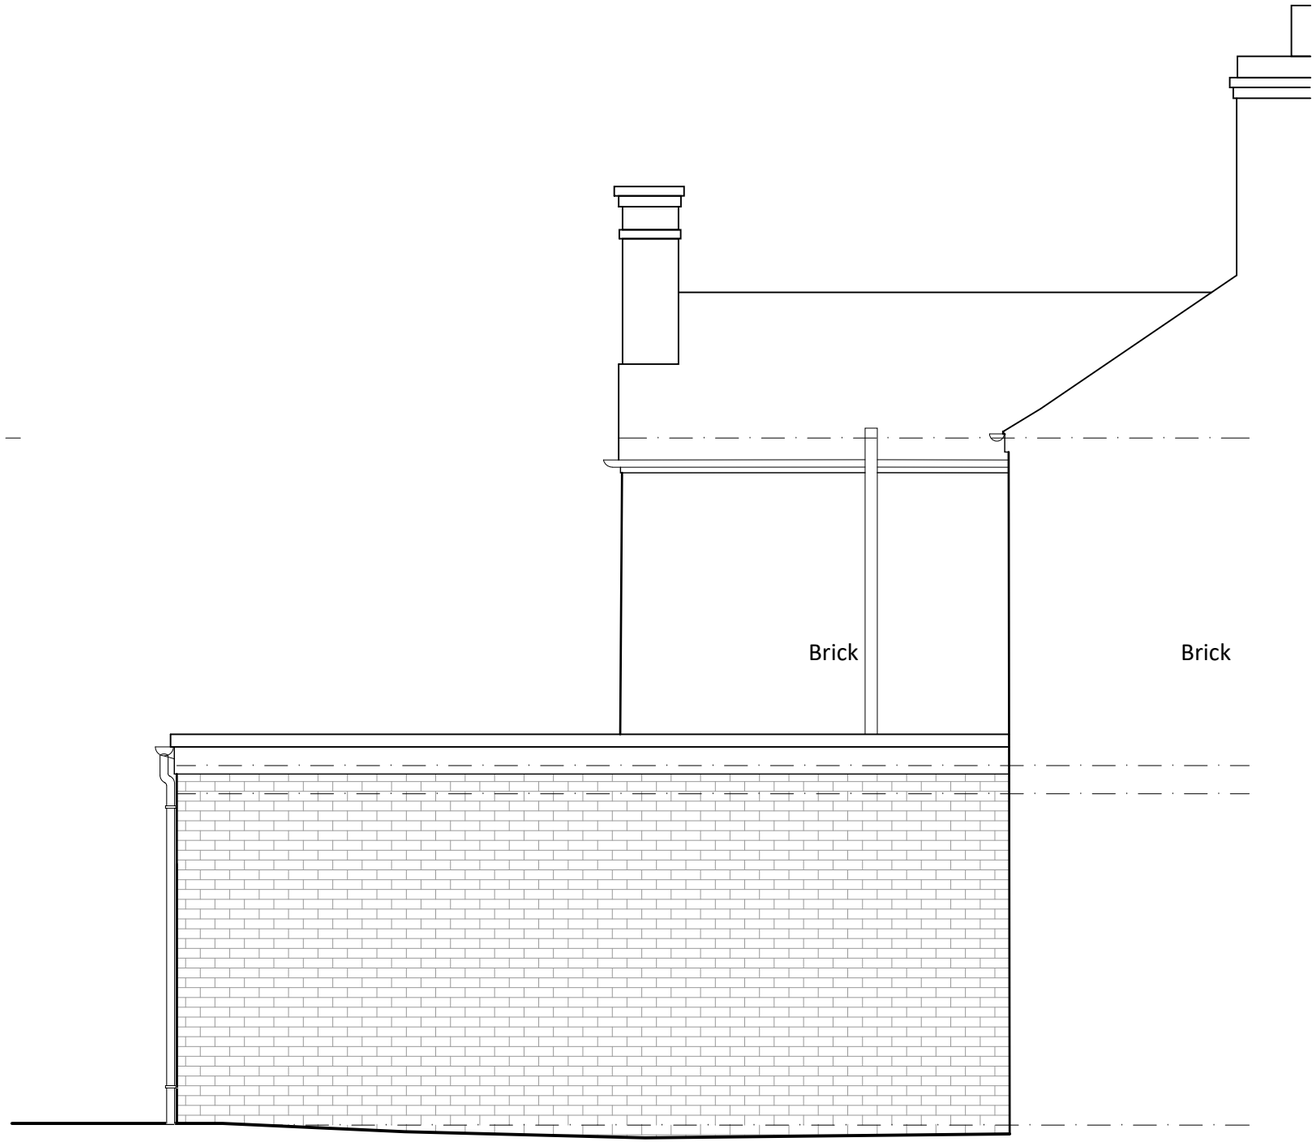

Proposed Side Elevation

1:50 Scale

0 0.5 1 2 3 m

The copyright of this drawing is vested in S&S Architecture (UK) Ltd & is not to be reproduced, copied, or used for any other purpose than intended without the prior written consent of S&S Architecture (UK) Ltd.
The electronic version of this drawing is to scale on an A3 sheet. Each scale stated refers to the drawing above it, so if anyone prints this drawing please ensure that it has been printed at the correct size (A3) & not 'Scaled to Fit'. Scale bars have been provided for the purpose to check this, so if the bar scales do not scale correctly the drawing sheet has not been printed correctly.
Preferably use figured dimensions (if shown) and report any discrepancies to S&S Architecture (UK) Ltd immediately.

S&S Architecture (UK) Ltd

Architecture

T : 0121 382 5959

M : 07989 648867

E : stephen@sandsarchitecture.co.uk

www.sandsarchitecture.co.uk

Client	Mr Sidwell - 309 Highbridge Road, Sutton Coldfield, West Midlands. B73 5RB
Dwg	Proposed Elevations
Scale	1:50
Date	Dec. 2024
Dwg No.	2025.013-04a